ARCHITECTURAL


PORTFOLIO

NICHAPA EAMCHAROEN




selected work 2022-2026

table of contents

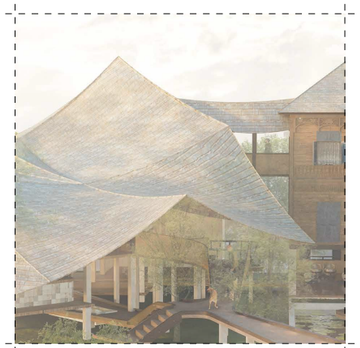


01

Living Heritage
: Interior Project

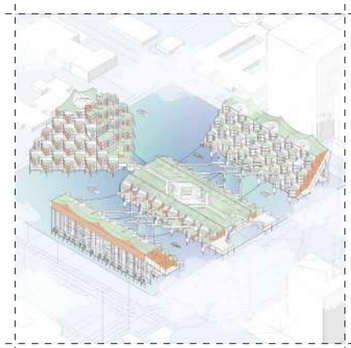


02

Village in a City
: Residential Project

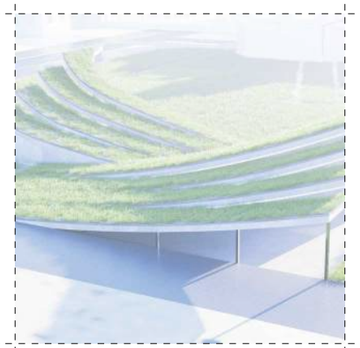

03

Flow
: Museum

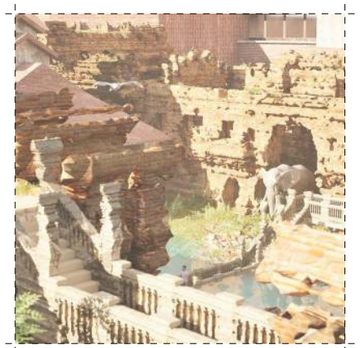

04

Invisible Boundaries
: Extrastatecraft



05

From Street to Neighbourhood
: Mix-used building

01


Living Heritage


a culinary sanctuary in Kudi Chin

Y4 S2
Brief: Retro-Pedagogies
Program: AI, PS, Rhino, Blender, Autocad, Sketchup

Living Heritage, a culinary sanctuary in Kudichin. Located in Kudi Chin, a neighborhood defined by the coexistence of diverse cultures and religions, this project investigates how architecture can facilitate pedagogical exchange through culinary practices. The proposal positions the house as a platform for both experiential and participatory learning, where locals engage with foreigners and Thai adults through shared cooking activities.The architecture creates an environment where knowledge is not only taught, but lived, practiced, and shared enabling exchange beyond the boundaries of language and belief.

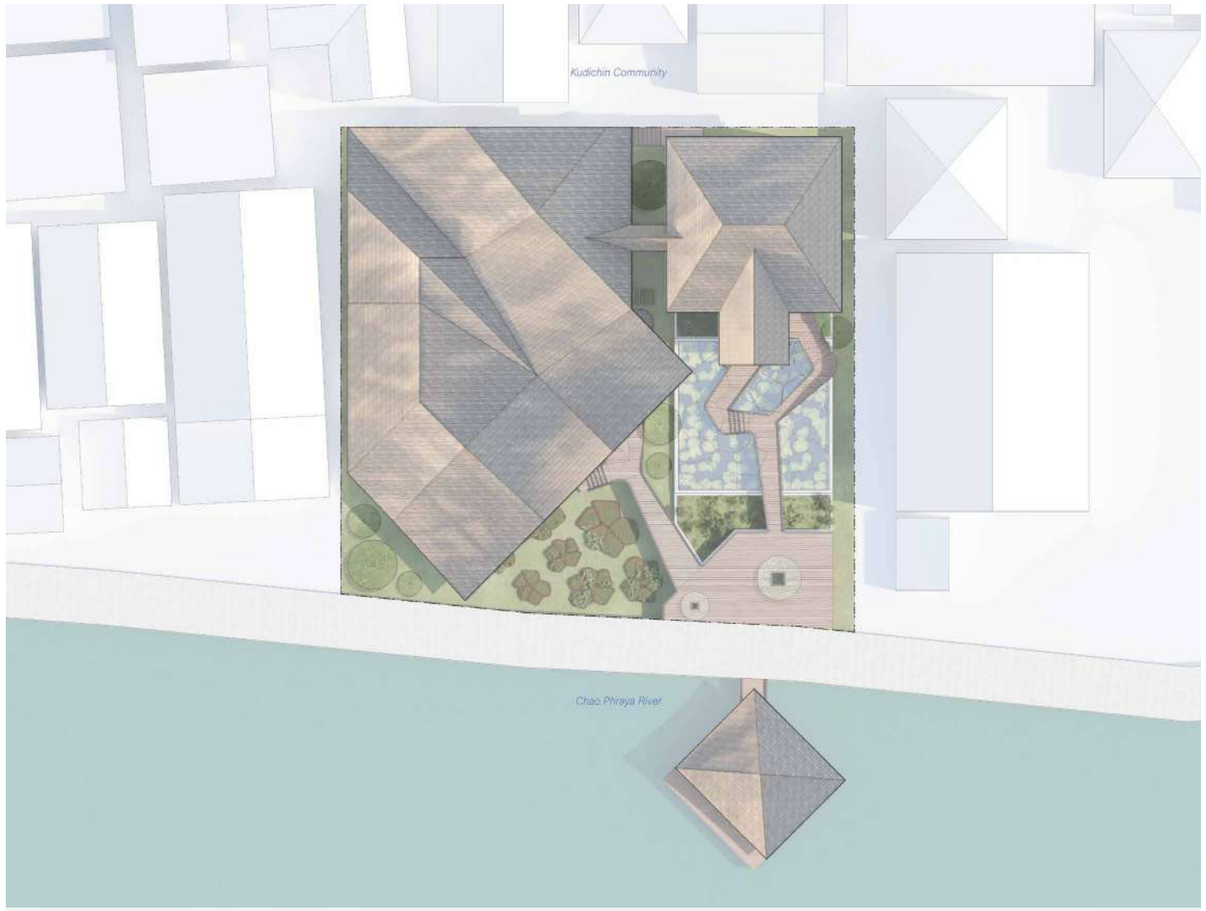



Kudichin Community
Chao Phraya River

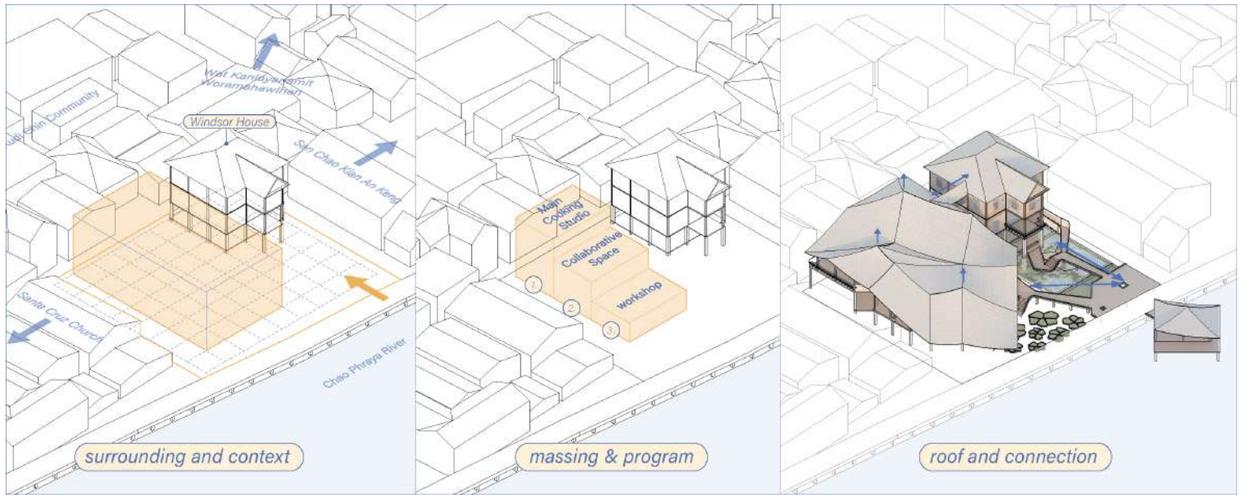
Wat Kanlaya Rangsarit Woramahawihan
Kudichin Community
Windsor House
Soi Chao Kiam An Neng
Santa Cruz Church
Chao Phraya River
surrounding and context
Main Cooking Studio
Collaborative Space
workshop
massing & program
roof and connection







main kitchen
reception
dining area
temporary workshop
theoretical & workshop
exhibition display area
kitchen garden terrain
cafe & stall
floating farm
water lilies pond
outdoor lounge
pier

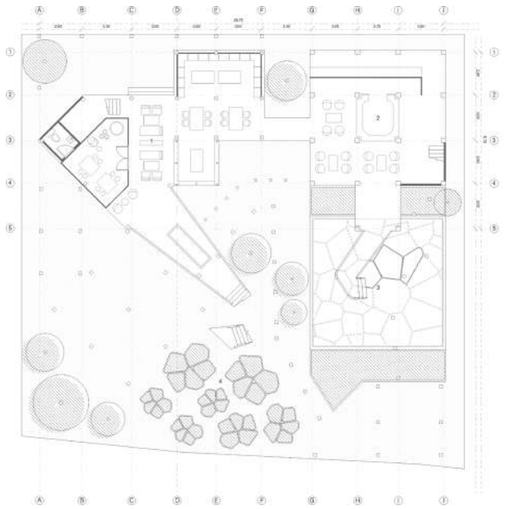


1. Temporary Workshop Area
2. Cafe & Stall
3. Water Lilies Pond
4. Floating Farm

ground floor

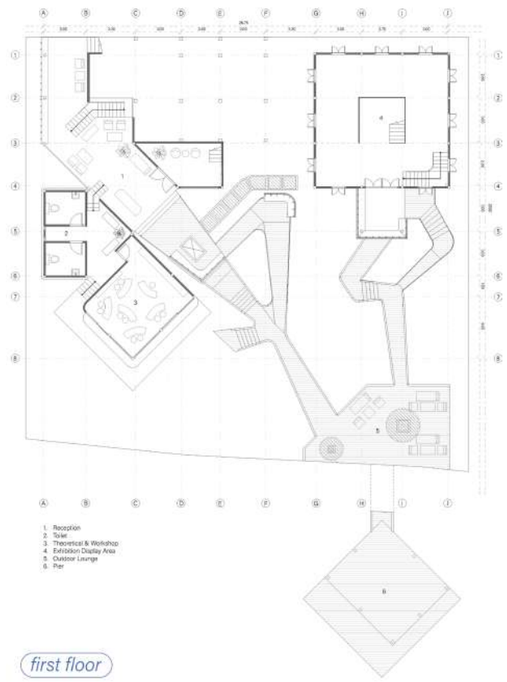

1. Reception
2. Toilet
3. Theoretical & Workshop
4. Exhibition Display Area
5. Outdoor Lounge
6. Pier

first floor

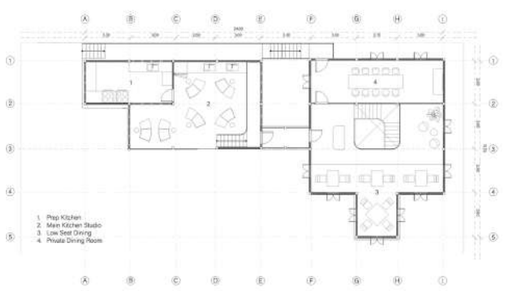

1. Prep Kitchen
2. Main Kitchen Studio
3. Low Seat Dining
4. Private Dining Room

second floor












The project is divided into two systems: a new extension for program-based learning, including workshops and a main kitchen studio, and the preserved house for experience-based learning through dining, observation, and cultural interaction. Together, these spaces create an environment where knowledge is not only taught, but lived, practiced, and shared beyond language and belief. Cooking becomes a pedagogical tool—knowledge is transmitted through hands-on practice, storytelling, and repetition. The kitchen is not enclosed; it is visually open, allowing learners to observe techniques before participating.

02

Village in a City

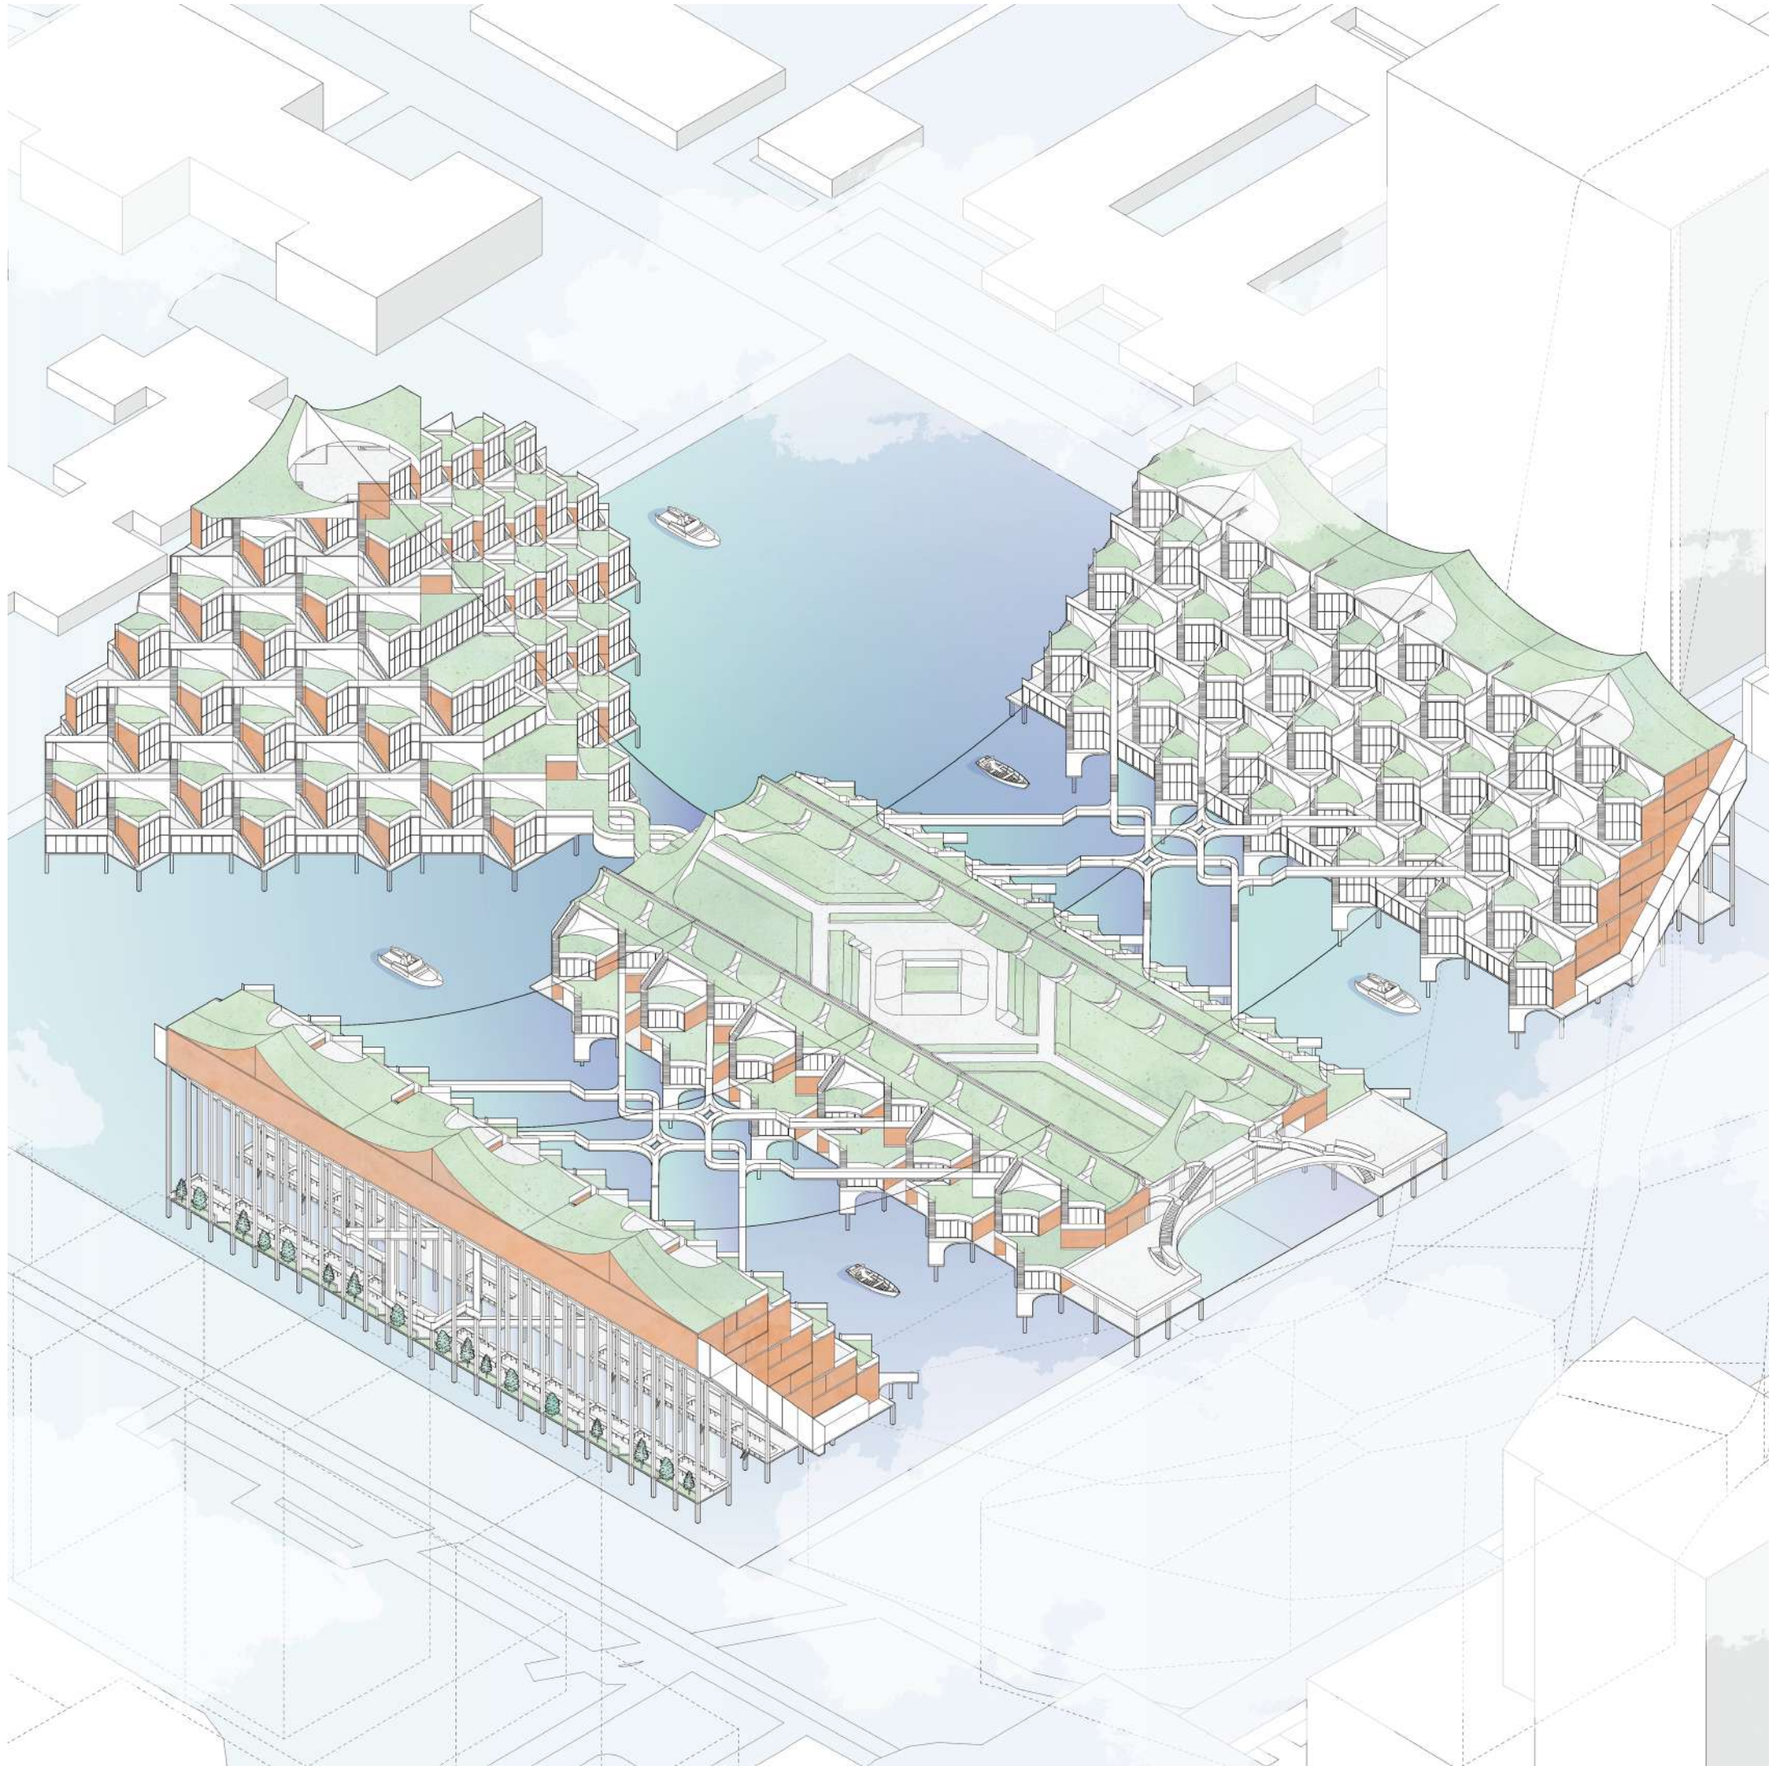


Y3 S1
Brief: Urban Incubators
Program: AI, PS, Rhino

Village in a City is a Thai modern residential project located in the heart of Ploenchit, an area surrounded by high-rise and mixed-use buildings that blend work and living spaces seamlessly. The project aims to break the norms of the area by mentioning new activities, creating a space for relaxation and community gatherings, staying true to the original spirit of the neighborhood. The design emphasizes cultural exchange, reflecting the diverse population brought by the embassies in the vicinity. Sports and parks are utilized as connectors. The residences are designed to accommodate both locals and foreigners.

OLD BRITISH EMBASSY

PLOENCHIT, BANGKOK




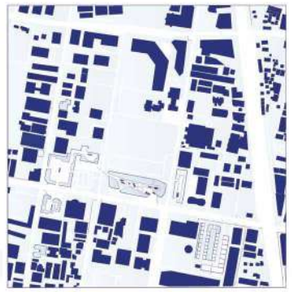





FLOW


PARK AREA

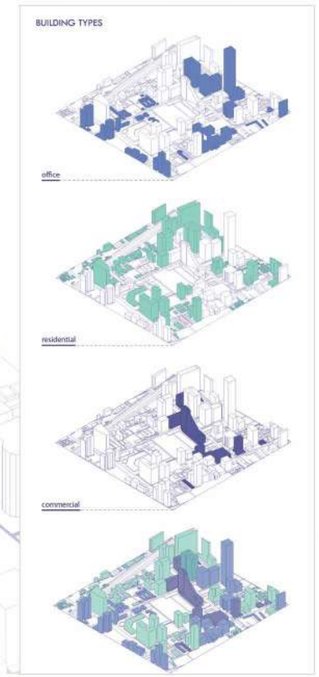


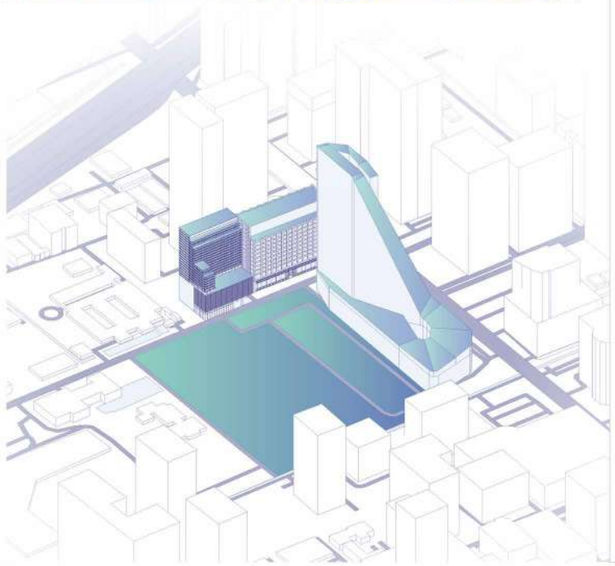


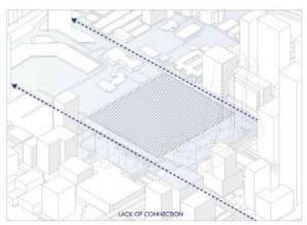





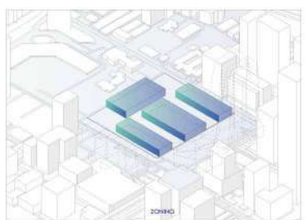


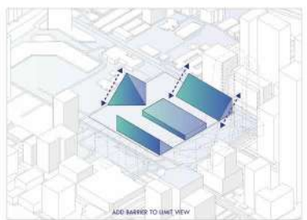


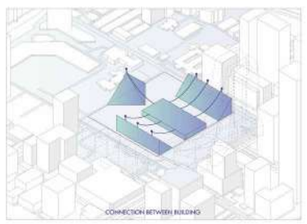


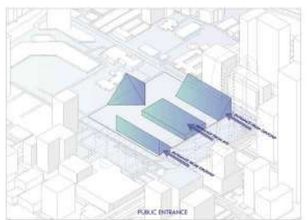


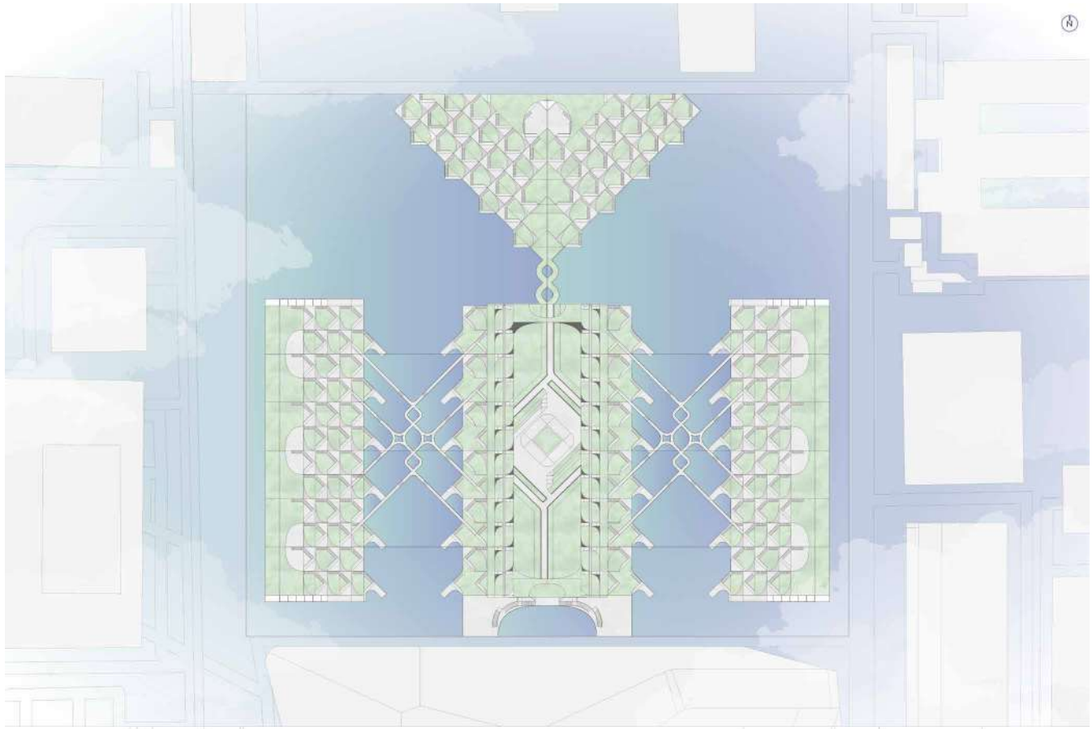

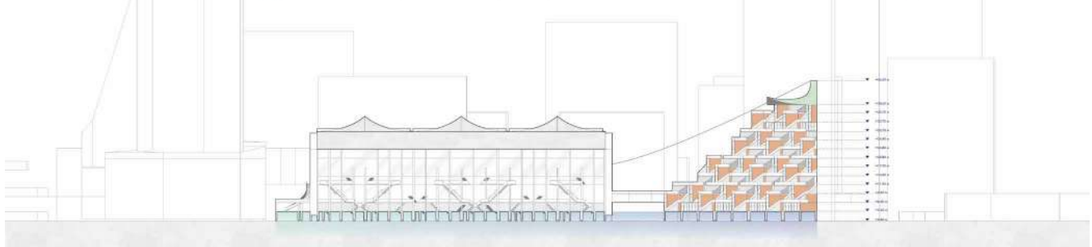

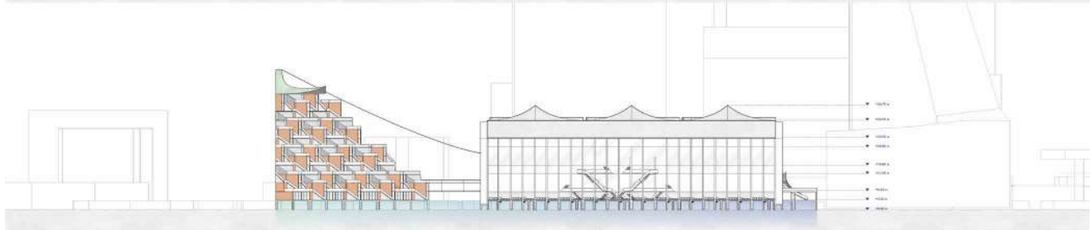

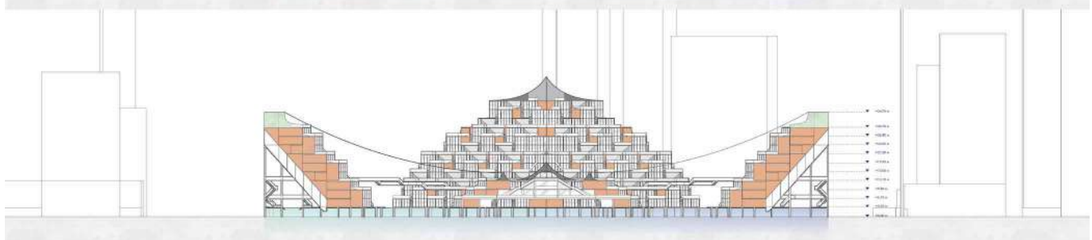

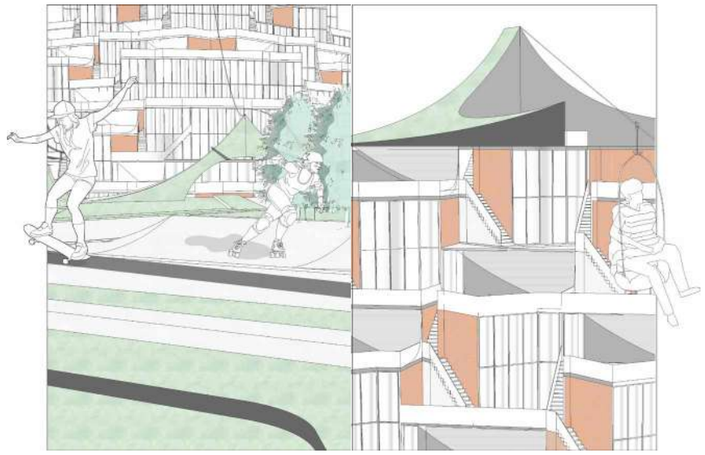






Due to its location surrounded by numerous embassies, the unit layouts are designed to cater to a variety of cultures. Each unit has been designed differently based on the needs of its residents, whether local or foreign, creating a diverse and inclusive residential community. The design thoughtfully incorporates elements that reflect the preferences and cultural influences of the occupants, ensuring a personalized and adaptable living experience. There are five types of units, with three main types located in the domestic area. At the top of this area is a communal park that can be used by both residents and the public. The private and public spaces are separated by distinct levels to maintain privacy while encouraging interaction. To support the concept of using parks as areas for cultural exchange, each unit is also designed with its own green roof, providing additional greenery and promoting sustainability.



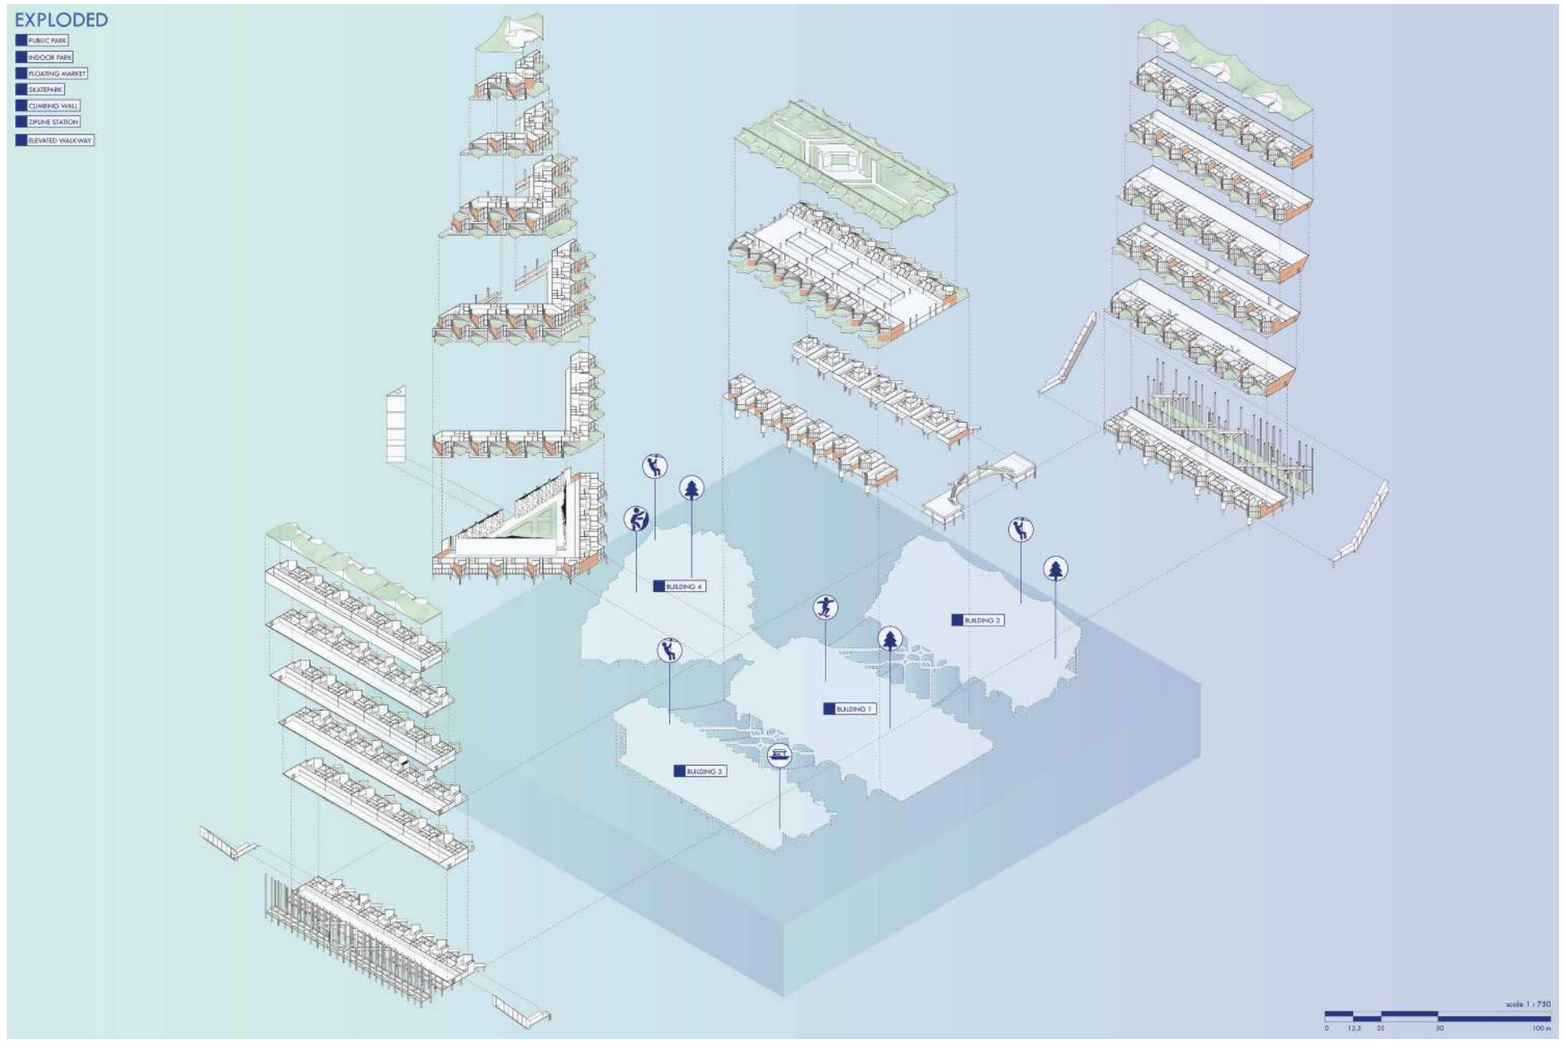





03
Flow


Y2 S2
Brief: Aquatecture
Program: Rhino, Blender, Ai, Ps


Flow is an underground living museum that highlights the importance of land use through many eras related to the waterway. The museum is placed in the underground level as an extension of Phayathai palace. It's different from the current museum in that it's a living museum people can experience through activities. The key concept is using the ground level to separate the timeline. In this area, water is the main factor that evokes the Ratchathewi area, but these days the importance of the waterway is lost. Flow is also created to bring back attention to the waterway.




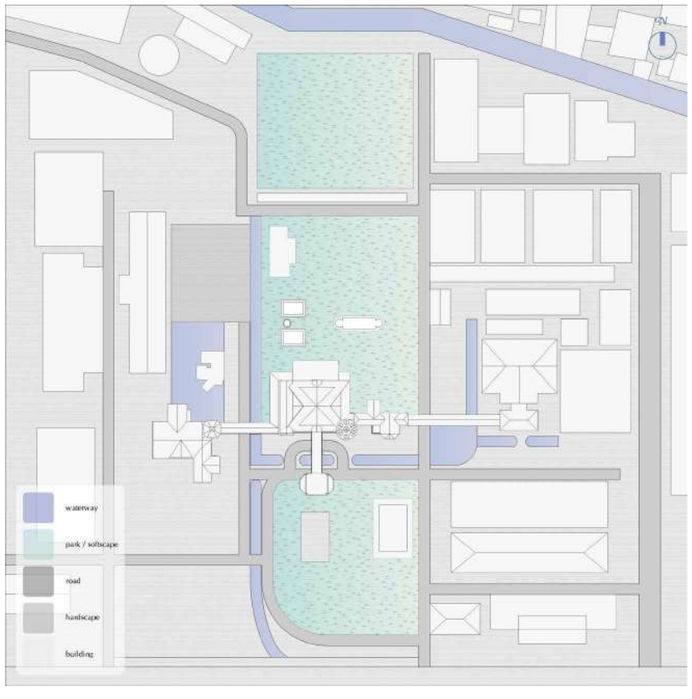


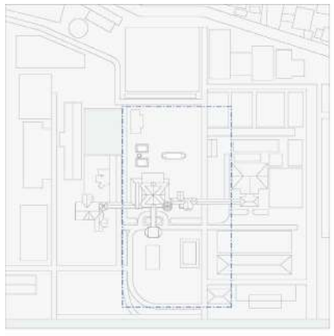


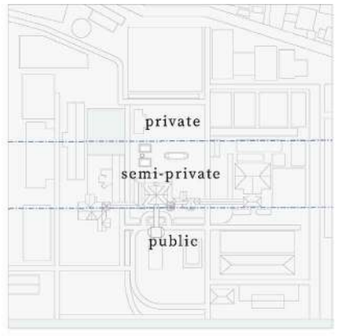

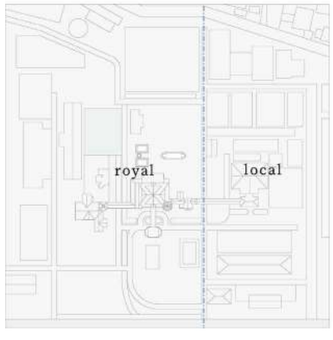

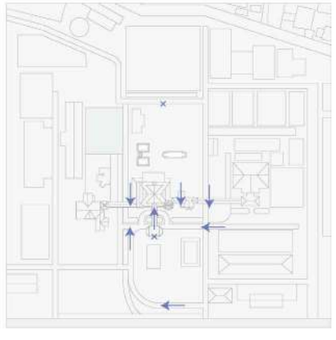


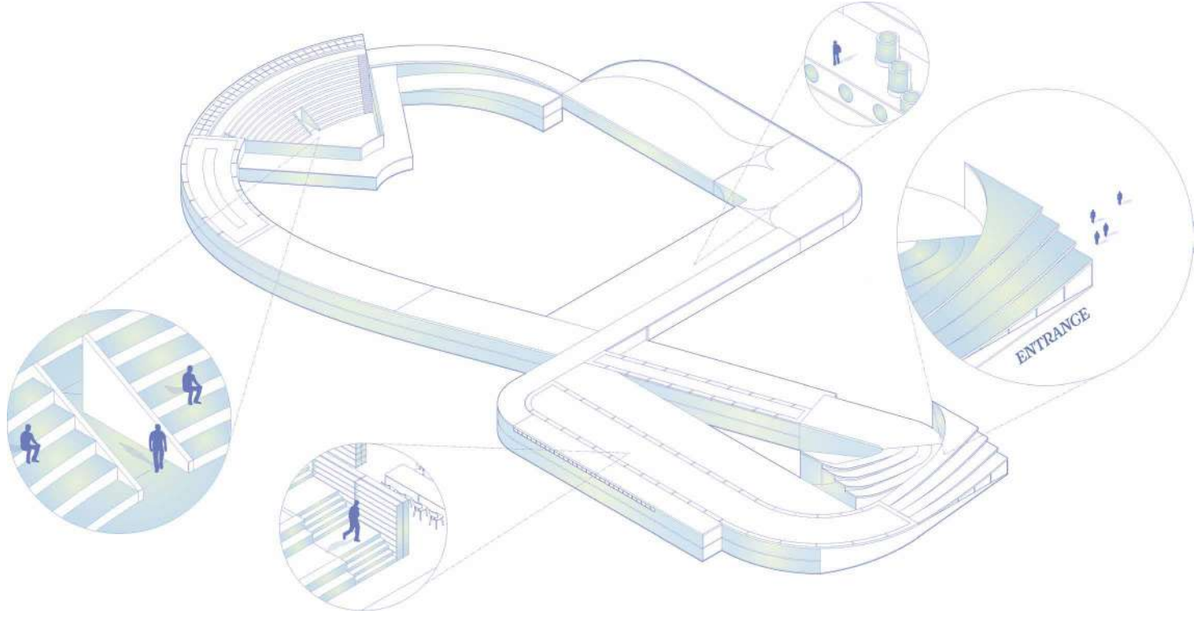

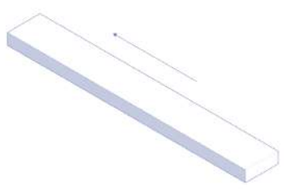


PATH

create a path through the palace

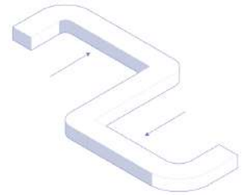


WATERWAY

create a shape follow landscape and waterway

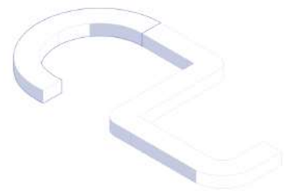


CENTRAL HALL

add extension for atriam

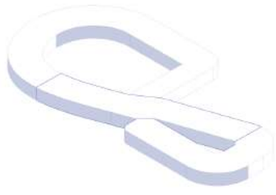


CREATE A LOOP

connext both side to create a loop

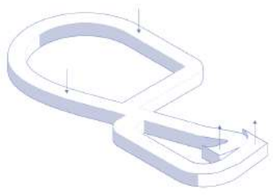


DEFINE


define level for normal ground and underground

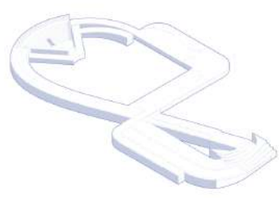


EXTENSION


extension on both width and floor level due to the use

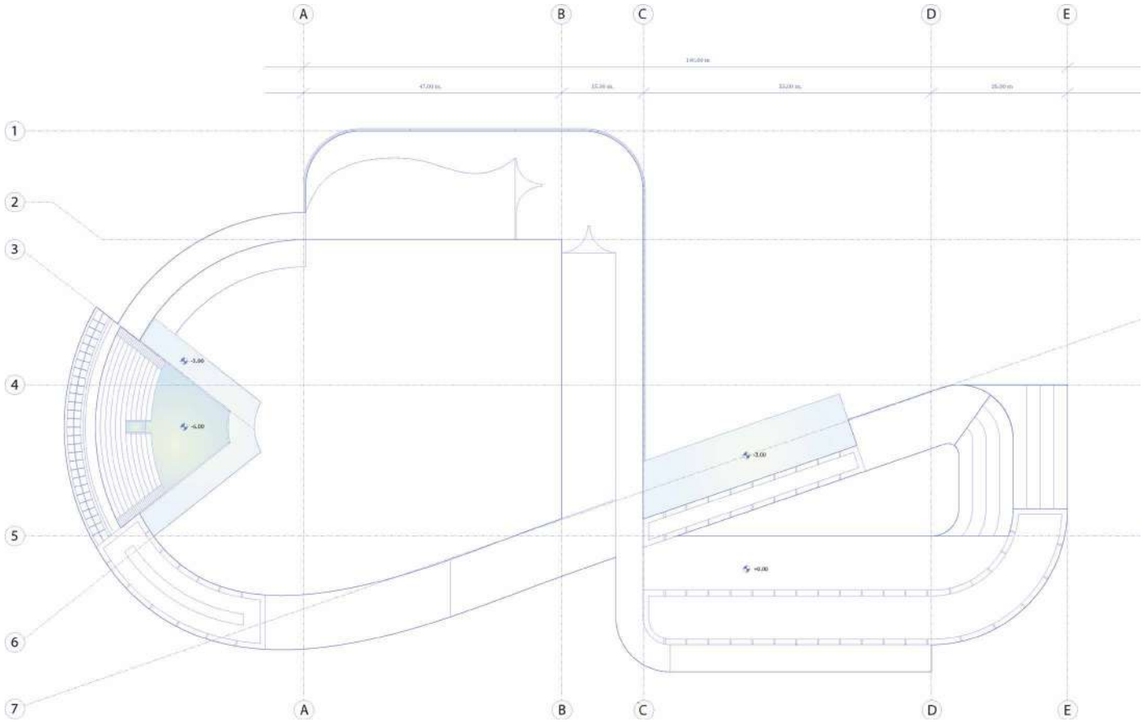

A
B
C
D
E
1
2
3
4
5
6
7
-3.00
-6.00
-3.00
+0.00

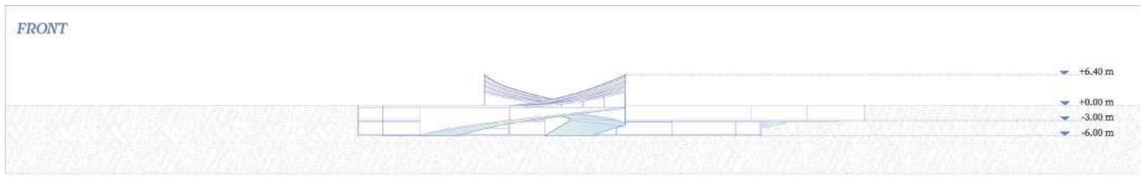
FRONT
+6.40 m
+0.00 m
-3.00 m
-6.00 m


SIDE
+6.40 m
+0.00 m
-3.00 m
-6.00 m

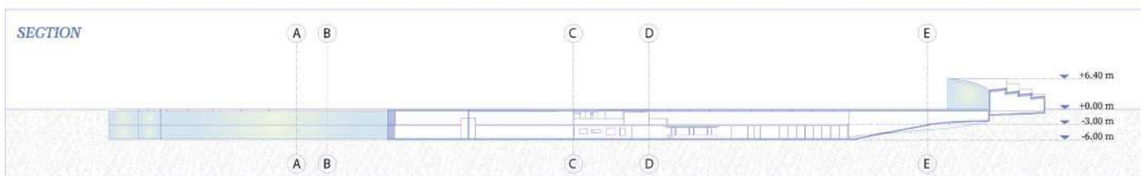
SECTION
A
B
C
D
E
+6.40 m
+0.00 m
-3.00 m
-6.00 m

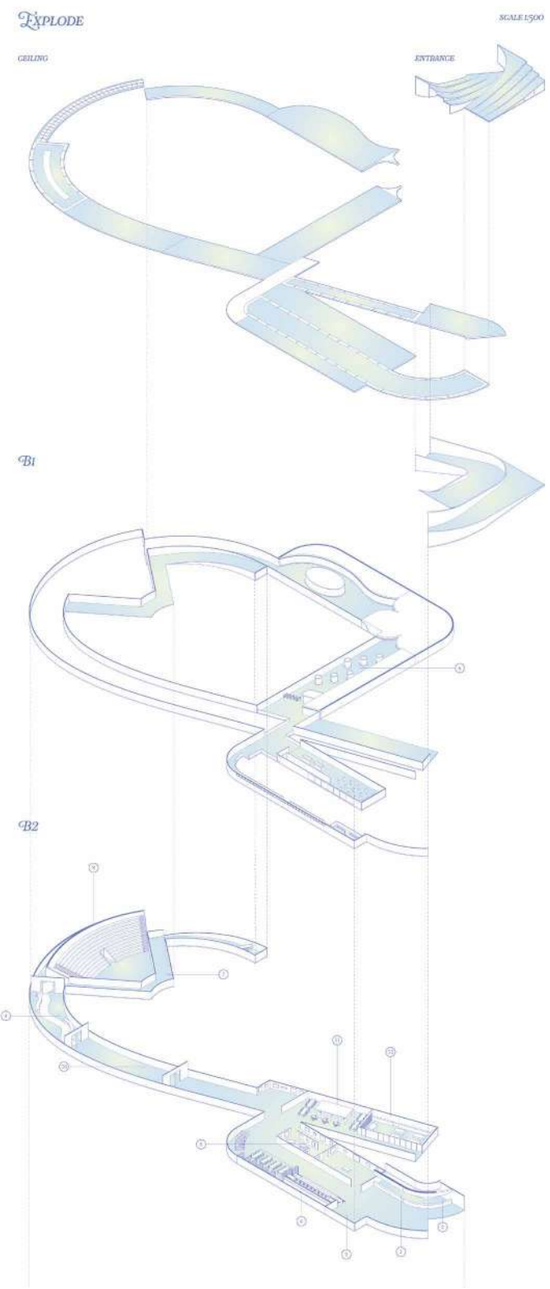
EXPLODE
SCALE 1:500
GEILING
ENTRANCE
B1
B2

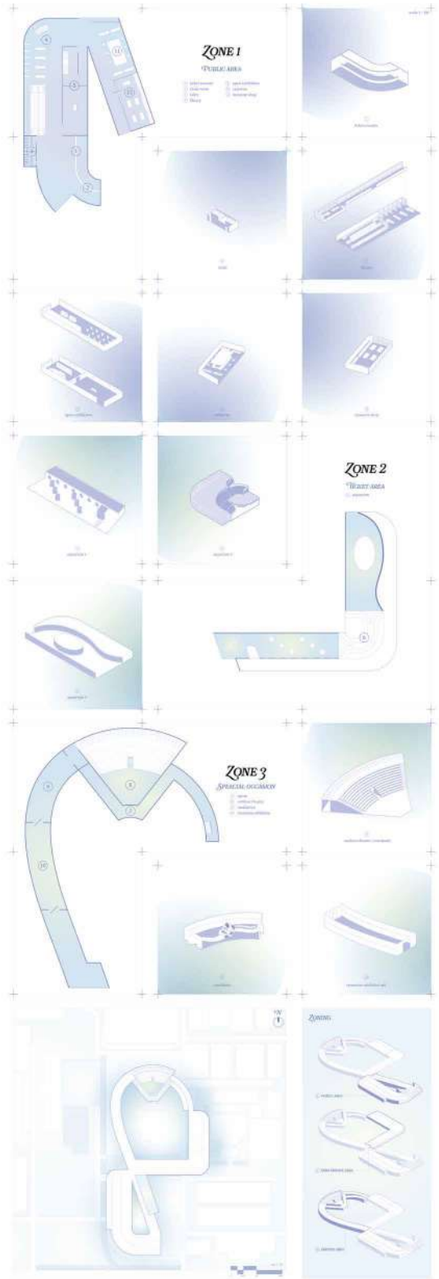
ZONE 1
PUBLIC AREA
ZONE 2
TICKET AREA
ZONE 3
SPECIAL OCCASION
ZONING









04


Invisible Boundaries

Rewilding Urban Zones in the Post-Anthropocene




Y3 S2
Brief: Extrastatecraft
Program: Unreal Engine, Rhino, Grasshoppper, Blender, Qgis, Ai, Ps, Ae


Invisible Boundaries act as an infrastructure that invites wildlife back to the city area, using ruins as an asset to bring nature into urban life. The project focuses on rewilding spaces and redefining the relationship between cities and nature. Instead of decoration, nature becomes part of daily life, creating shared spaces for humans and wildlife through four key invisible boundary methods.

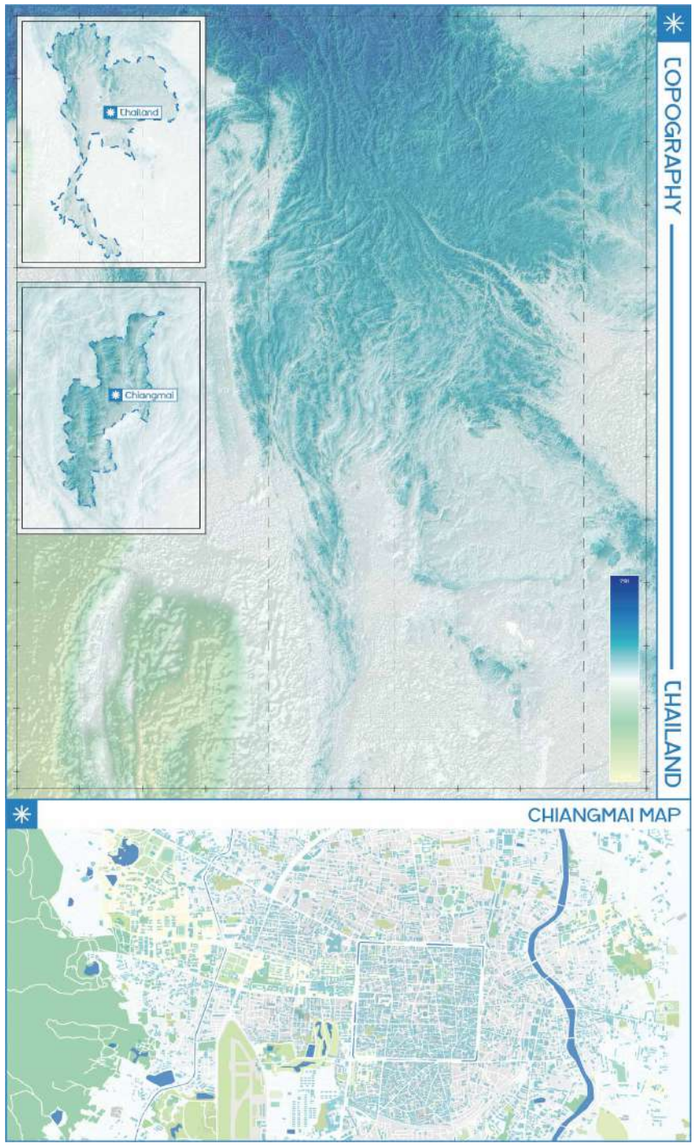


The project questions how we can introduce wildlife into spaces where most of the city is owned by humans. If we want to create a shared space, then how would we share a space. This leads to the idea of creating a new infrastructure as a terrain itself, using invisible boundaries both human-made and natural as connections that blend seamlessly. Ruins are introduced as key assets, following the Barry Walk concept of integrating nature into hybrid urban design. In the city, ruins make the most sense as they naturally invite plant growth, with grass and vegetation reclaiming these structures over time.

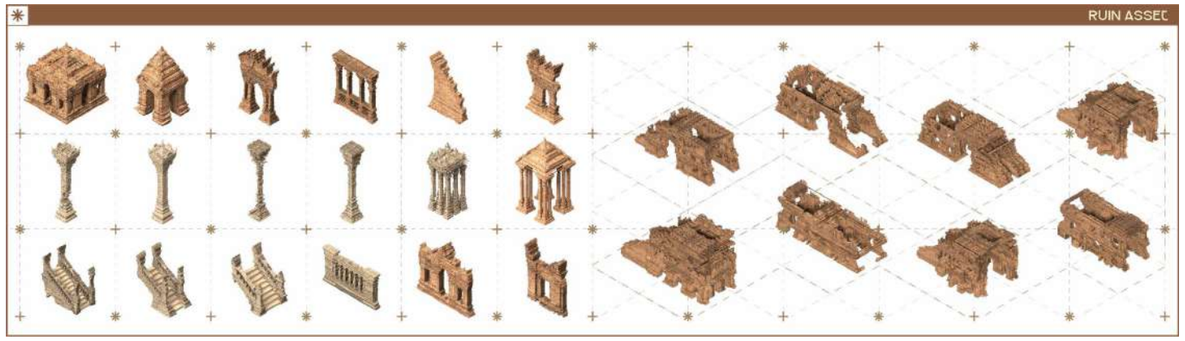



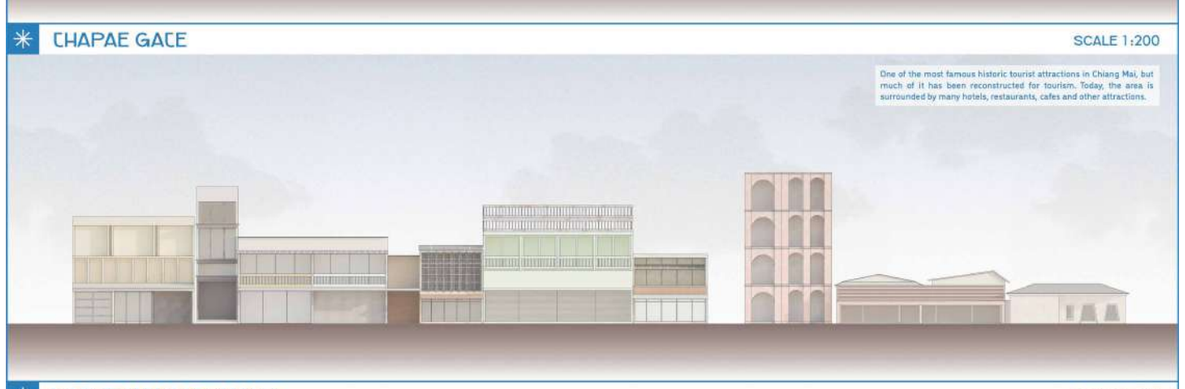

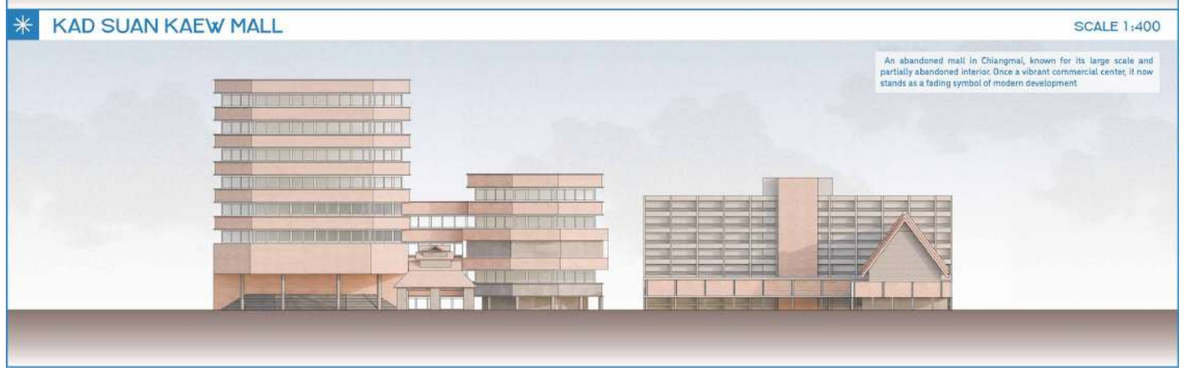



ONE NIMMAN





CHAPAE GATE

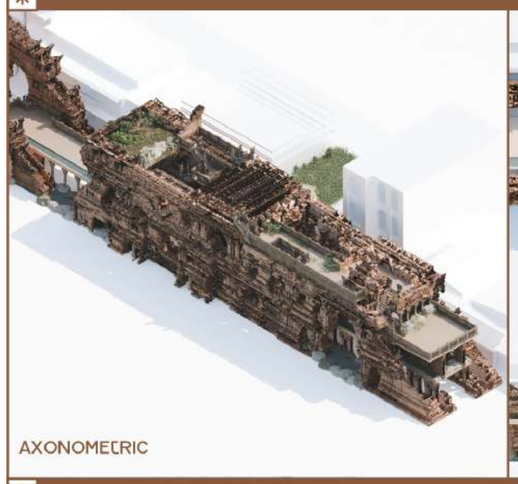


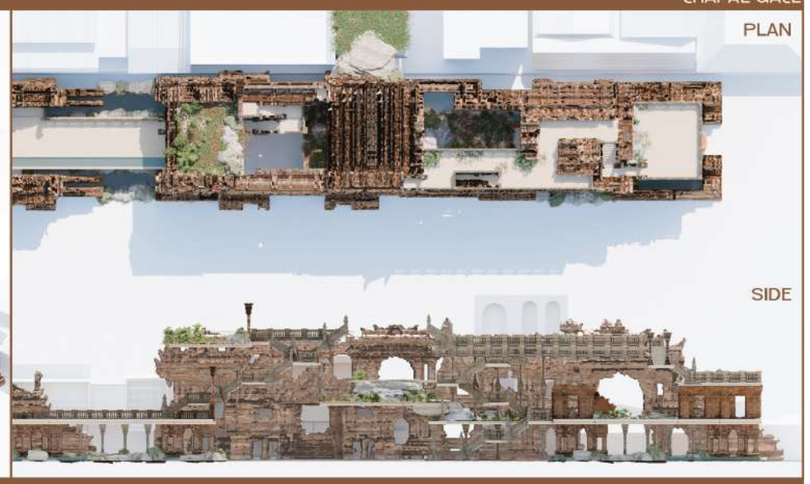

KAD SUAN KAEW MALL







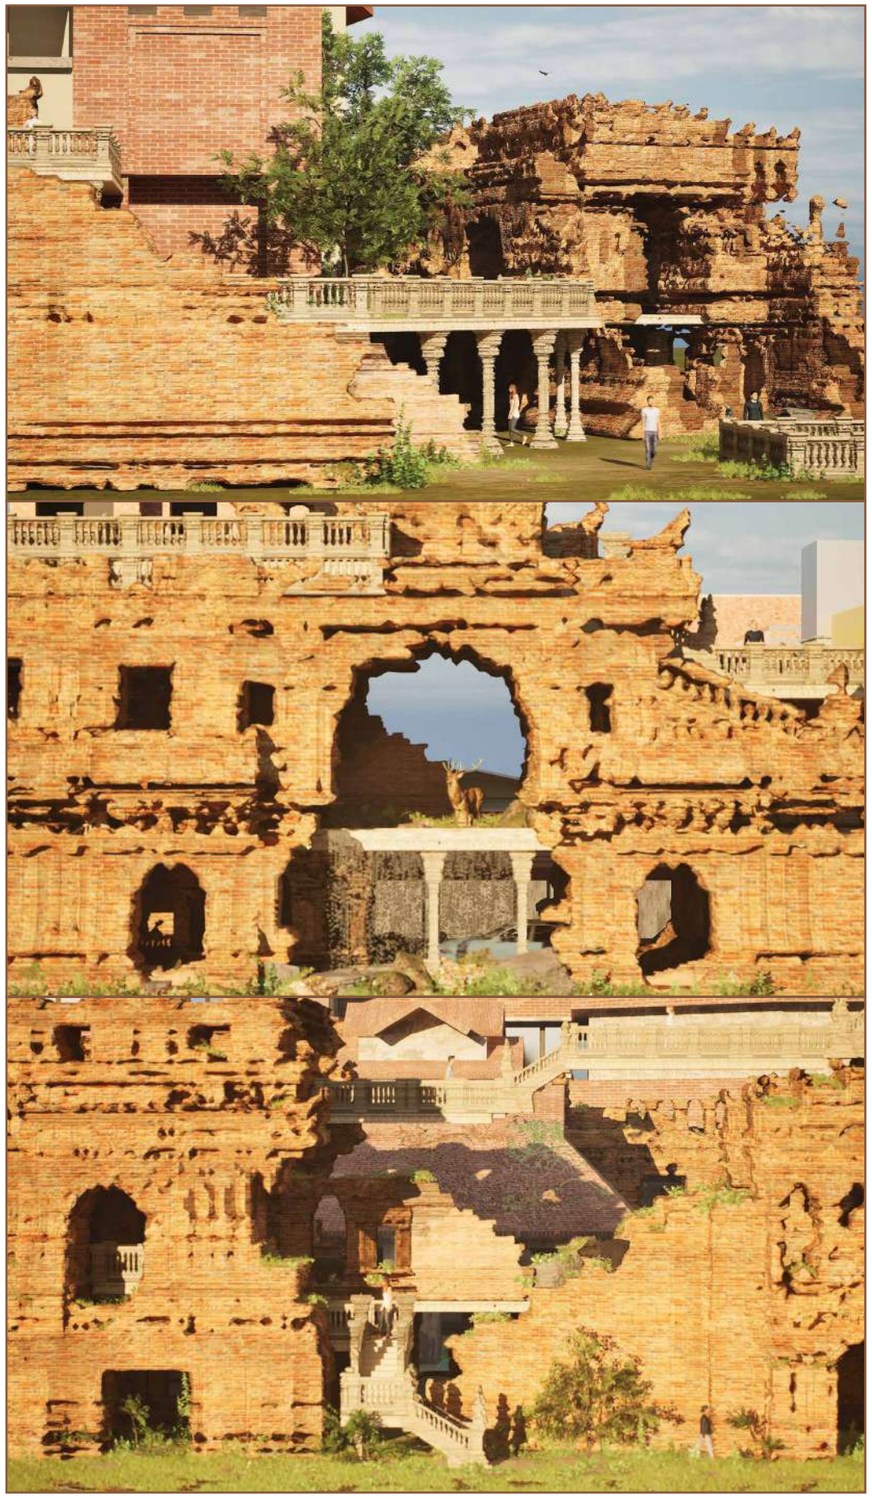




KAD SUAN KAEW MALL
Elevation Boundaries
Fluid Boundaries

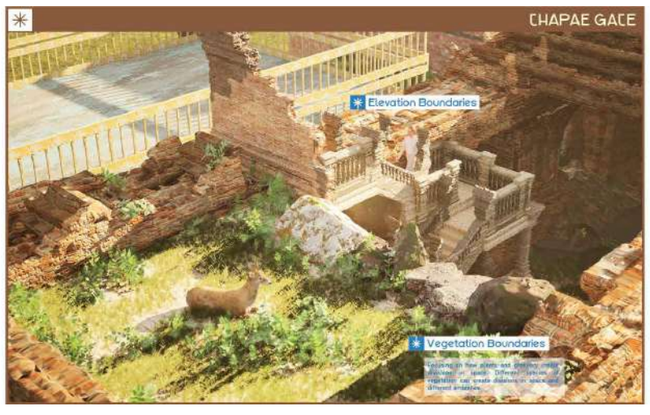
CHAPAE GATE
Elevation Boundaries
Vegetation Boundaries

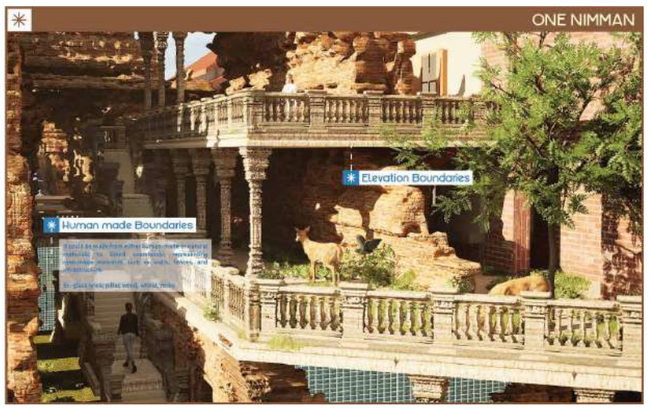
ONE NIMMAN
Elevation Boundaries
Human made Boundaries

05

From Street to Neighbourhood

Y4 S1
Brief: Pattern Language
Program: Rhino, Blender, Qgis, Ai, Ps,


From Street to Neighbourhood: A Field of Fragments is a mixed-use project in the Harajuku–Omotesando area that activates the plot by reassembling fragments from the existing urban context. The project creates a smooth transition between commercial and residential areas while maintaining clear boundaries between the two.



Pattern Language


brings the existing element that found in the site to create a strategies to apply for the new build

Urban Skin and Core

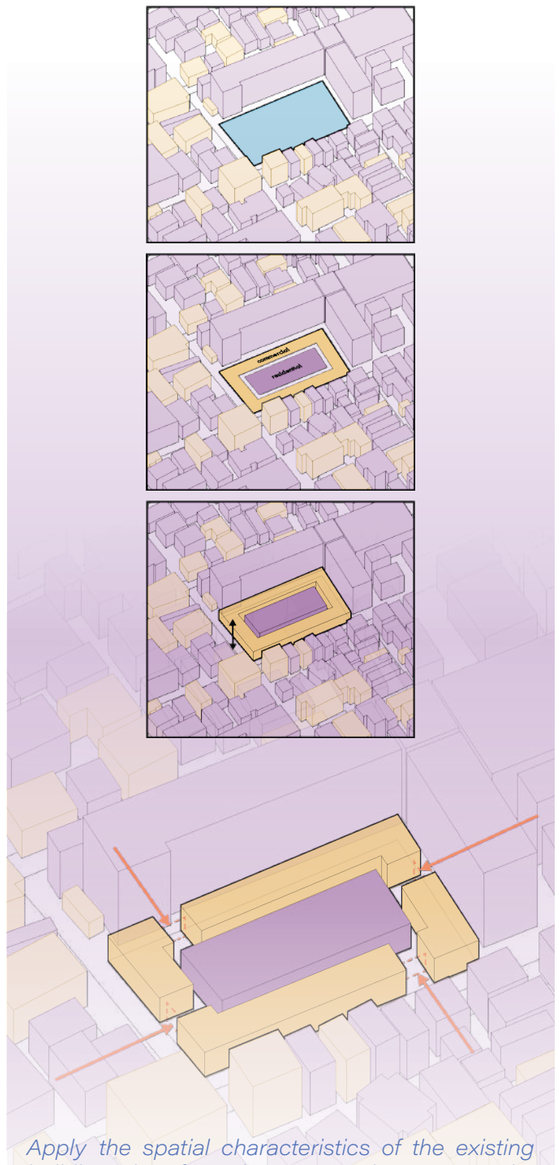


Apply the spatial characteristics of the existing building plots from the more active route to the site and its surrounding areas. By adapting the successful mix of commercial "skin" and residential "core," the design aims to activate the less frequented route and enhance pedestrian flow through the site.

Field of Fragments

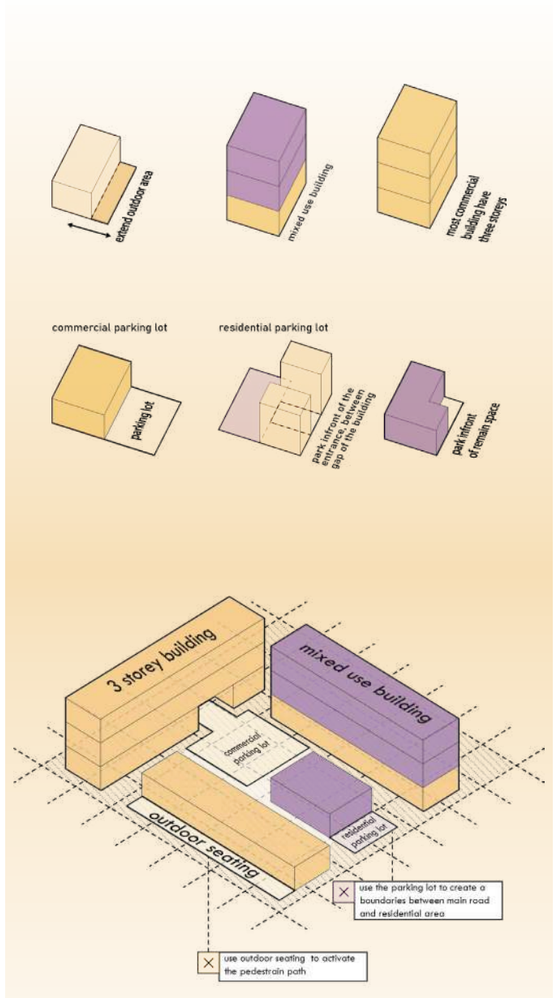



This strategy activates the block by reorganizing the plot layout using existing efficient elements observed from the site. Yet, these could be rearranged following the position of each block. Through this configuration, fragmented plots are transformed into a more active urban block.


Topographic Mass Adaptation

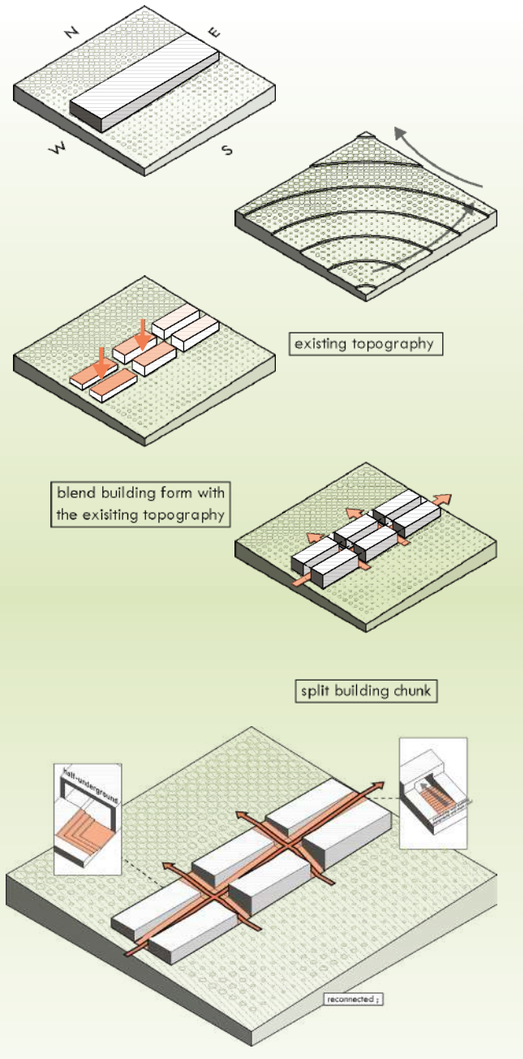


Reconfigure large building masses by splitting them to create new pedestrian paths that link the main road to interior alleys. The architecture itself becomes a transitional device, adapting itself to the existing topography.

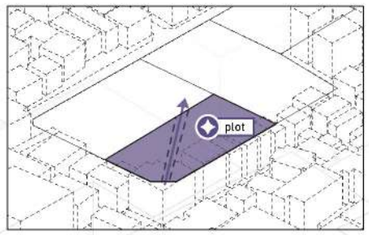

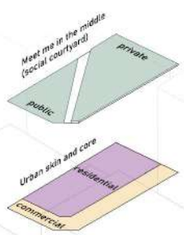


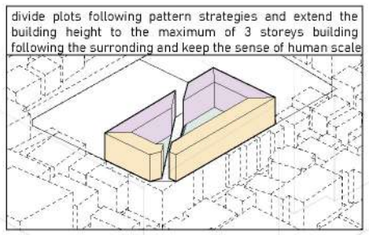


divide plots following pattern strategies and extend the building height to the maximum of 3 storeys building following the surronding and keep the sense of human scale

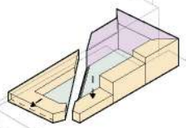


adapt the height follow the topography and extend outdoor spaces

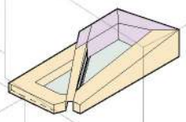


framed view and create a connection

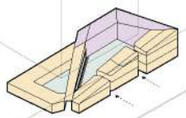



divide plots and create more entrance

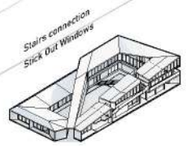


apply stair as a facade and extend window following the pattern strategies

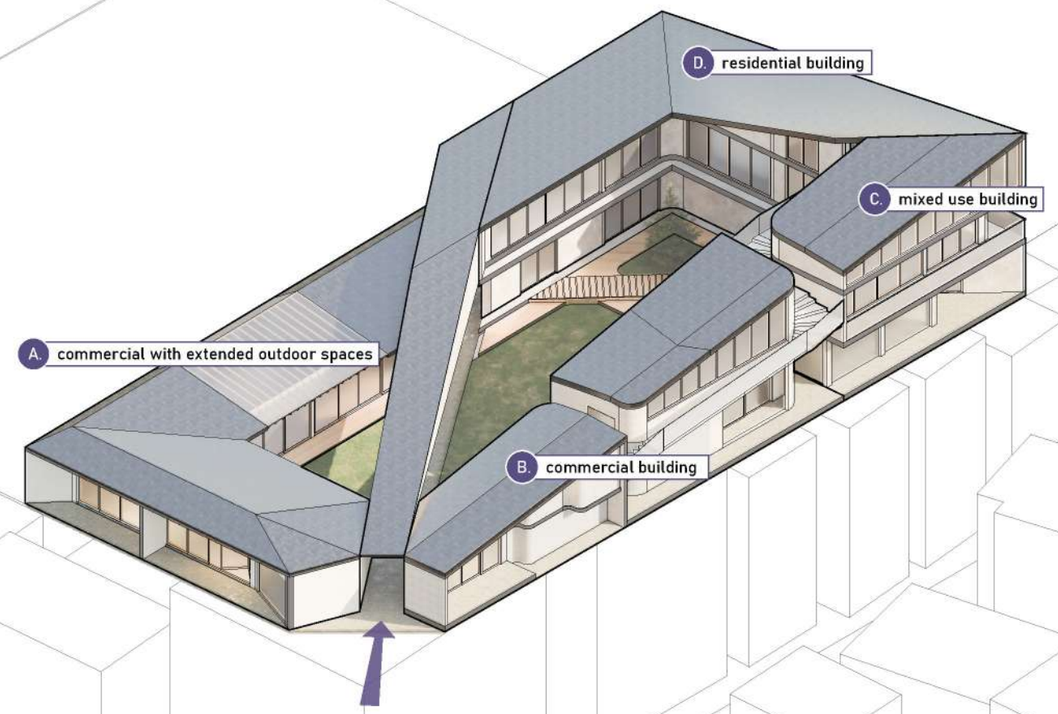

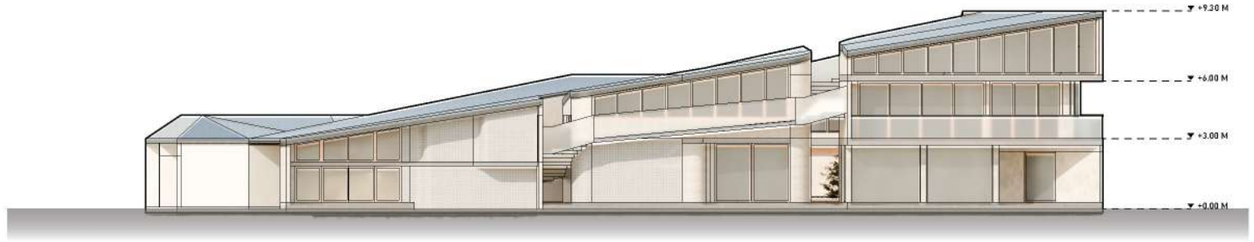

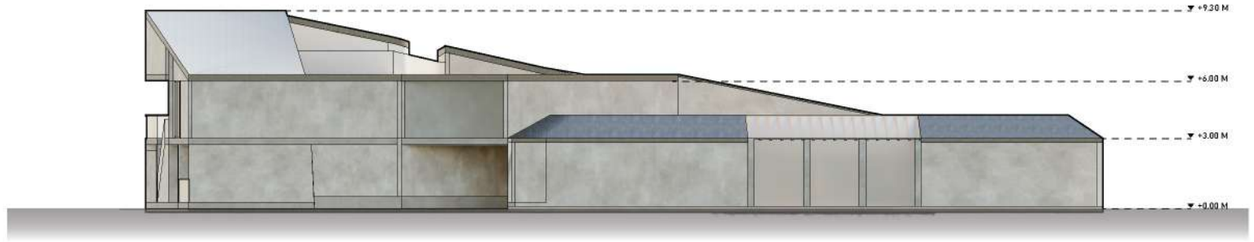

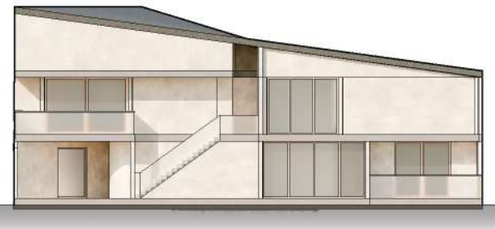





ONLY HUMAN STUDIO


Architectural Intern · Bangkok · 2026

A design studio working across architecture, interior, furniture, and structural design. The internship involved contributing to different stages of projects across a range of building types, including residential, parking garages, clinics, and cafés. Tasks included interior layouts, furniture design, lighting and material selection, structural modelling, technical drawings, diagrams, rendering, model making, and site visits.

The experience focused on human-centered design and attention to detail, exploring how proportions can be adapted to actual use and how materials, structure, and construction details shape the quality of a space.

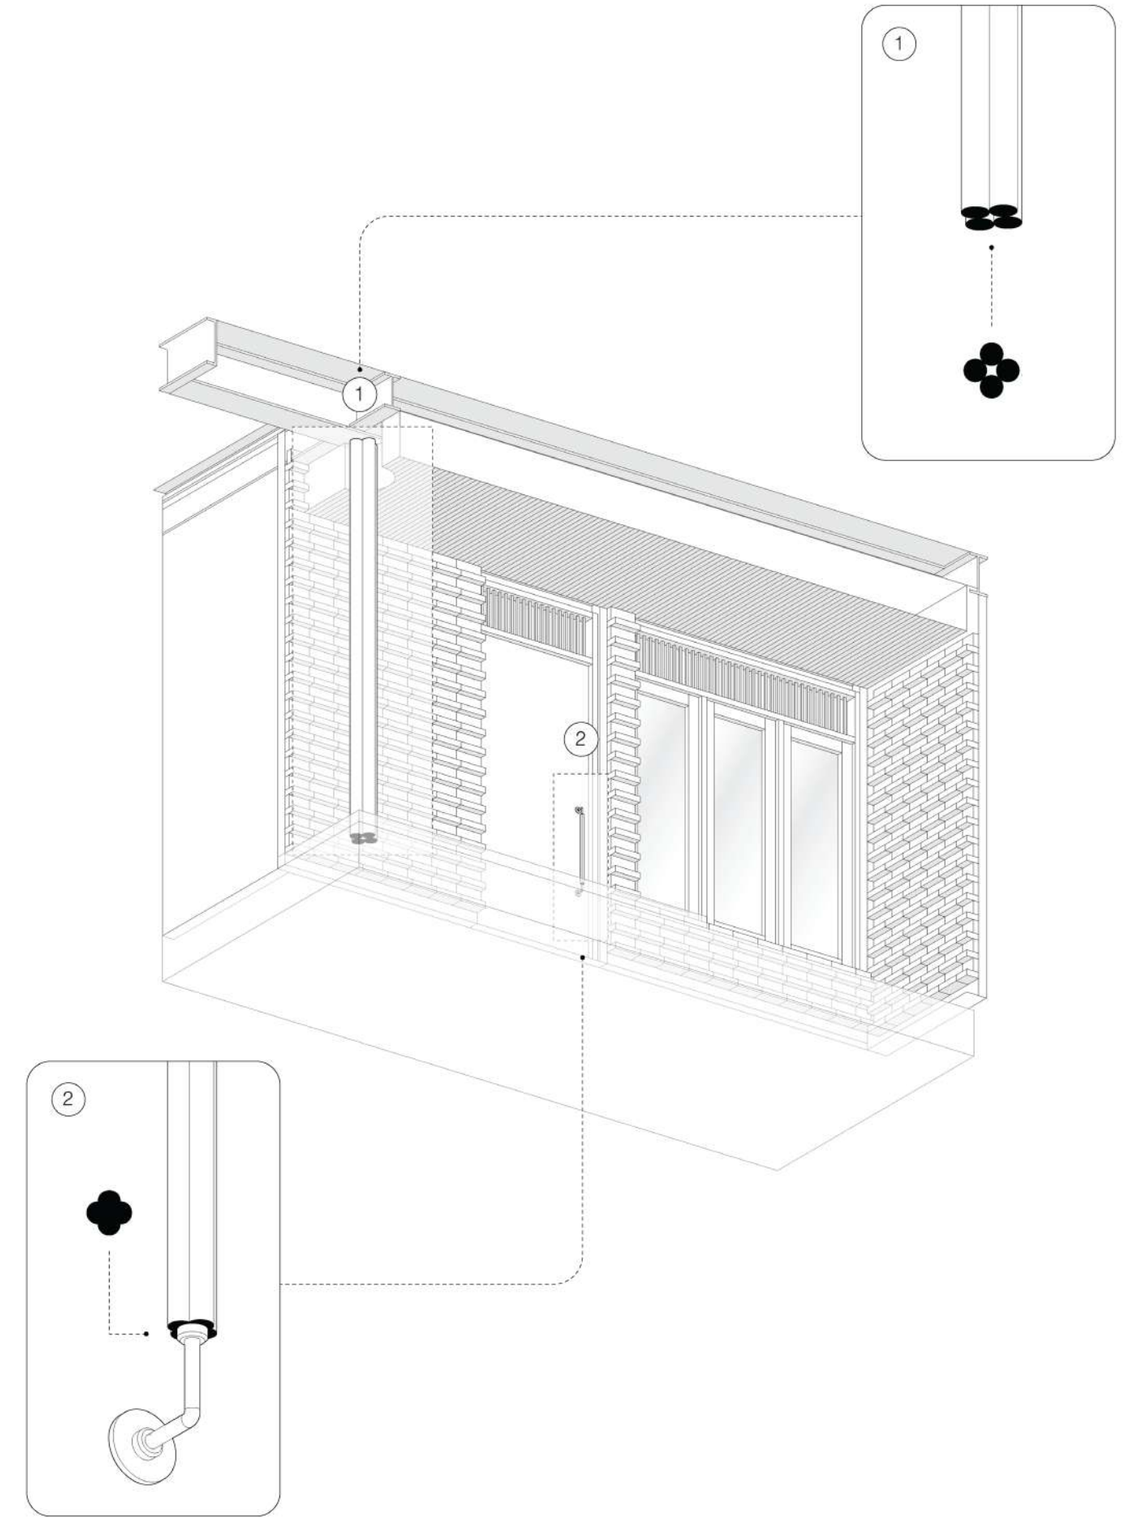

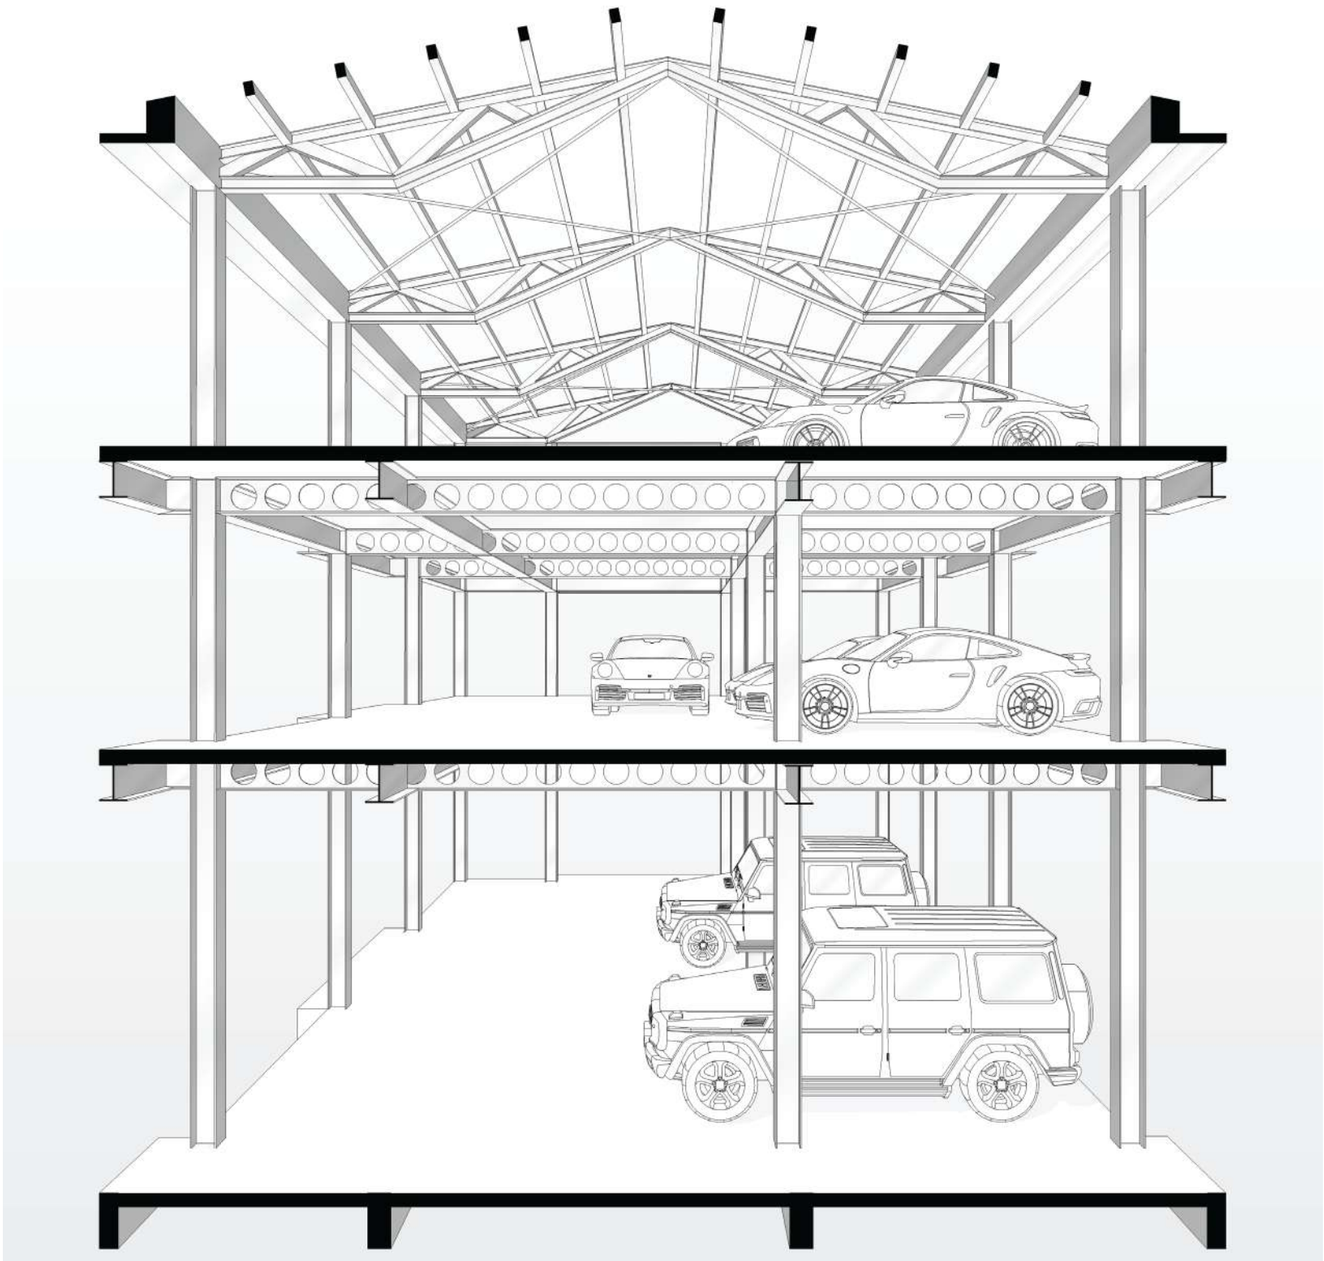

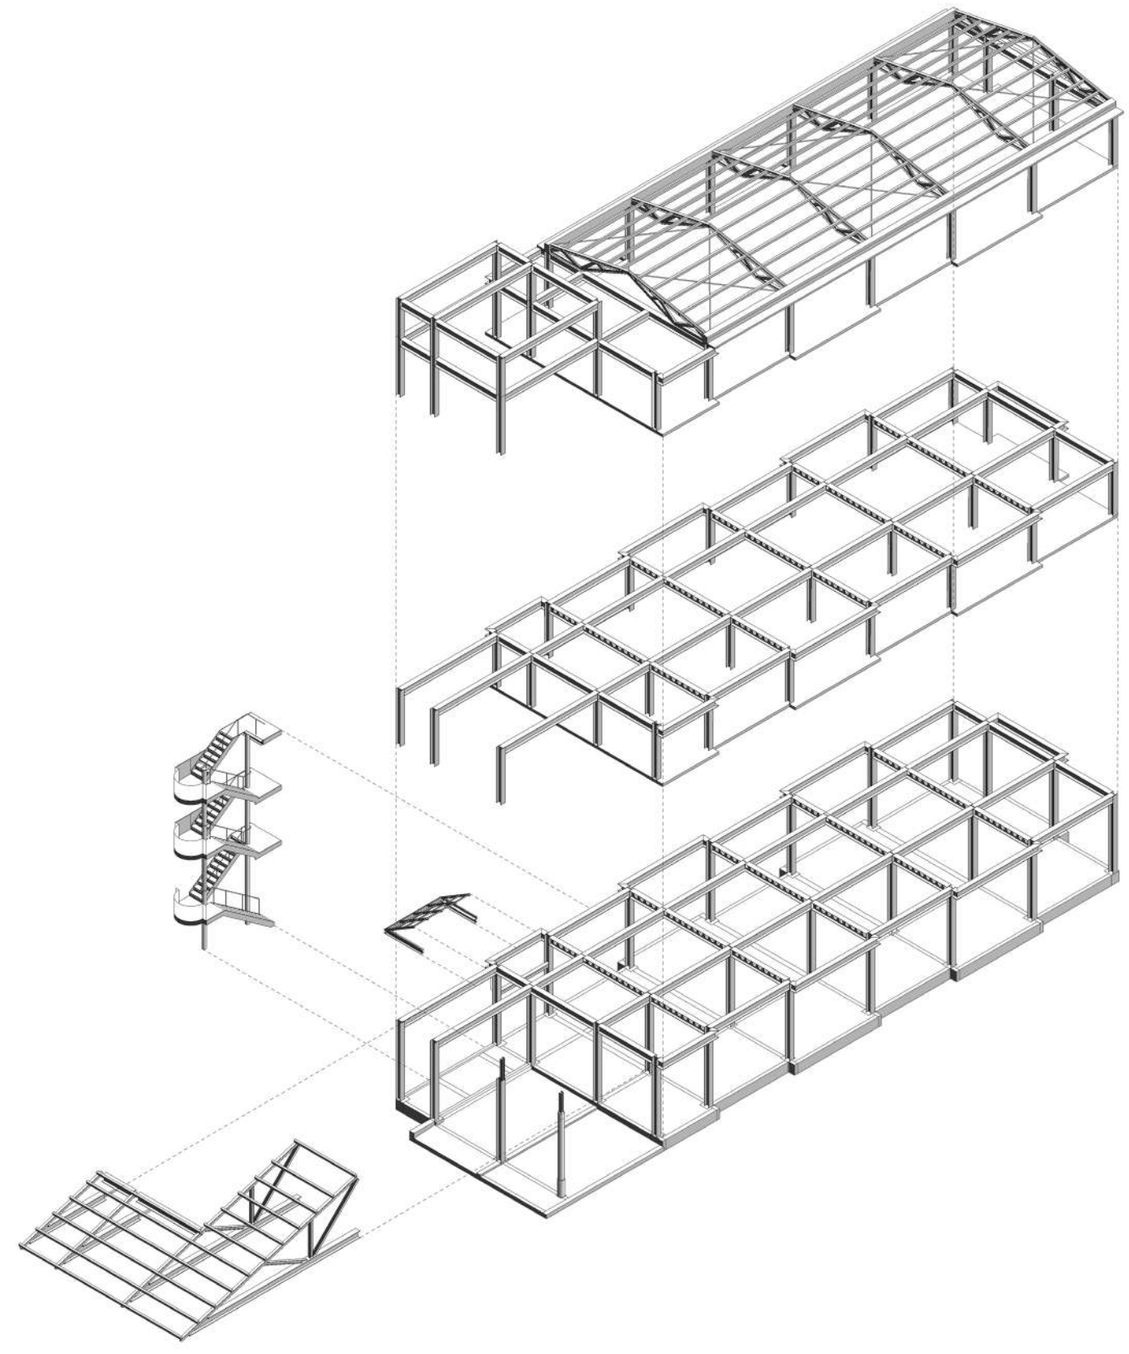

25G GARAGE — STRUCTURAL MODELLING & DIAGRAMS

Developed a 3D structural model from engineering drawings, studying the building's structural system, connections, and assembly from ground to roof. Translated the model into diagrams to communicate the structure and improve understanding of how individual components come together.

The garage uses a steel structure with cellular beams, where the shifted form creates slitted voids that allow indirect natural light into the space. In contrast, the office and residential buildings adopt a simple reinforced concrete grid, with structural elements left exposed to express their material character.



NNW CLOTHING STORE — INTERIOR DESIGN
Contributed to interior and furniture design, spatial layout, lighting, 3D modelling, and render visualization, with a focus on minimalist industrial elements and the balance between simplicity, materiality, and detail.




NNW CAFE&RESRAURANT — FURNITURE DESIGN
Contributed to the design of furniture pieces, including chairs, tables, and counters, with a focus on material selection, simplicity, and attention to detail. Explored proportions and dimensions in relation to human use, as well as the restuarant layout.

03 Diagrams & Visual Communication

HOUSE P


Produced diagrams illustrating the renovation, highlighting changes to the building structure, layout, and interior design.

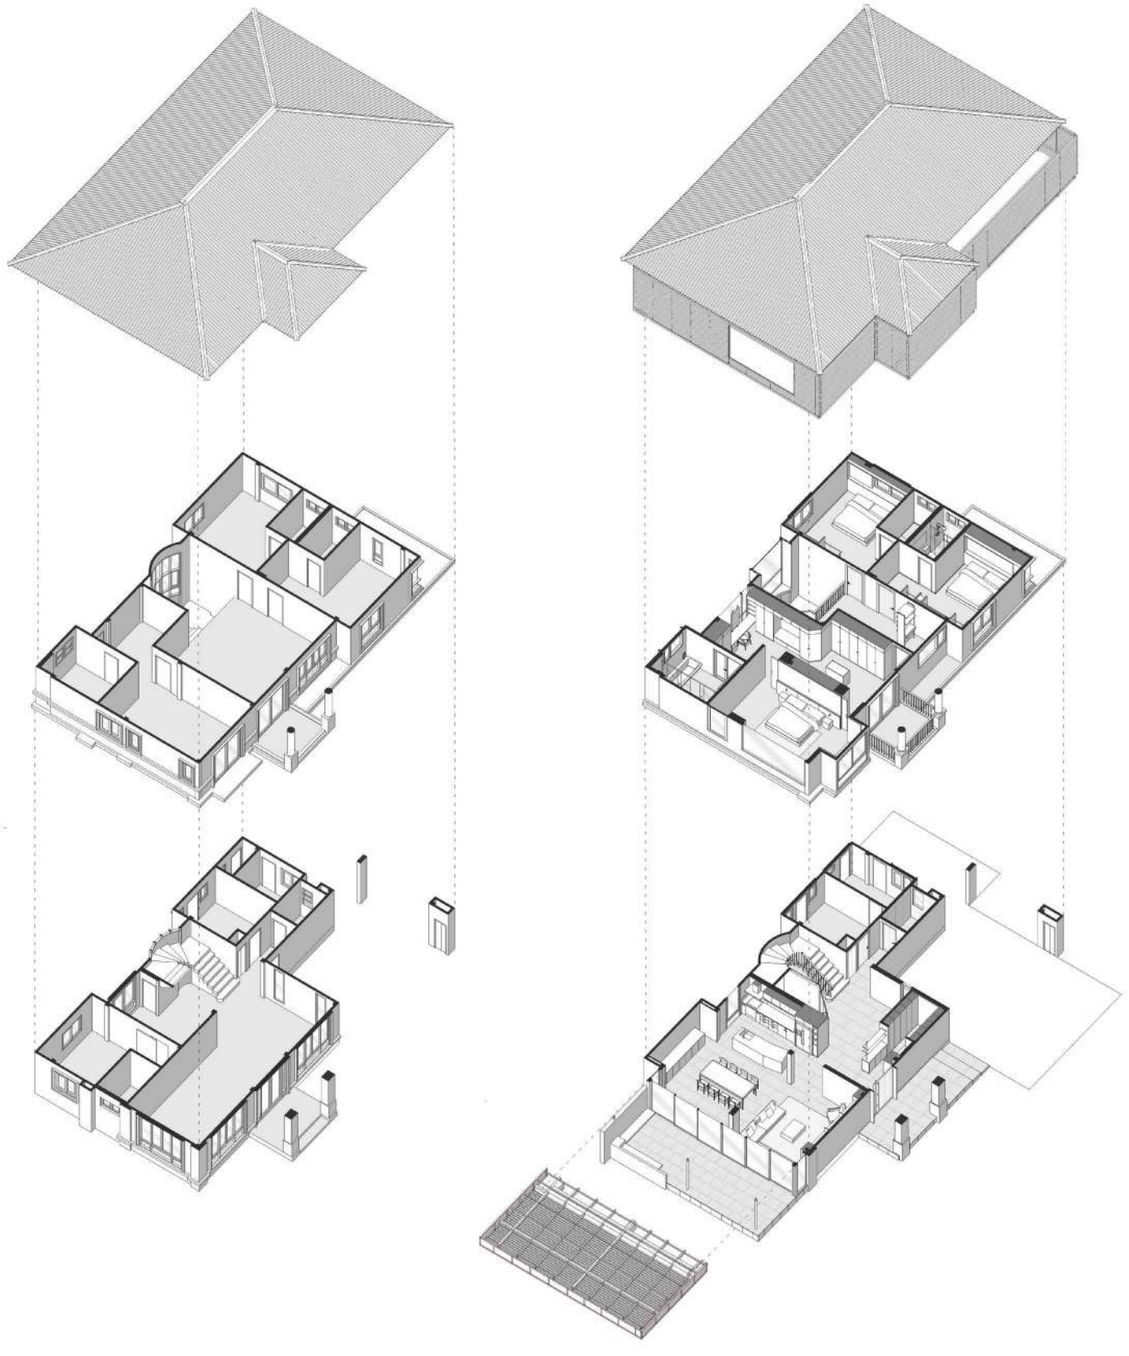

before *after*

DWCR APARTMENT

Produced diagrams illustrating interior and furniture design, highlighting material selections, textures, and spatial details.

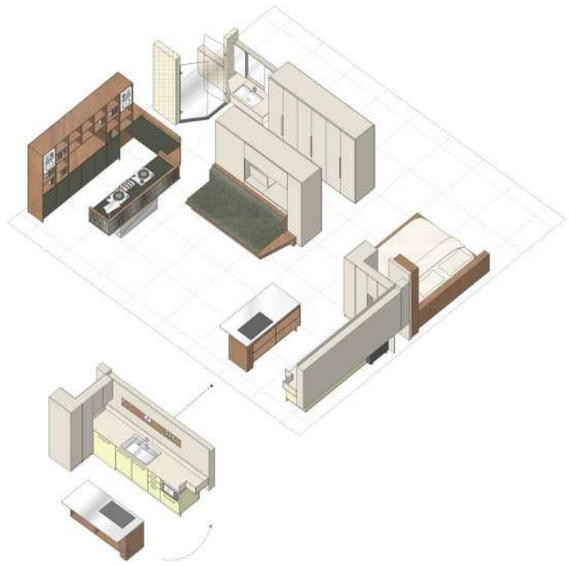



ASACHA MATCHA BAR

Illustrated furniture designs, material selections, and the overall interior design

