ARCHITECTURAL

PORTFOLIO

NICHAPA EAMCHAROEN



selected work 2022-2026



Nichapa Eamcharoen (Jinnie)

Architecture student at INDA, Chulalongkorn University, with international academic experience through an exchange program at Meiji University, Tokyo. Interested in parametric design, spatial experimentation, and conceptual design. Experienced in digital modeling and visualization using Rhino and Adobe Creative Suite.

Date of Birth: *05 Nov 2004*

Contacts
Phone number : +66 0842252211
Gmail : nichapa.jinnie@gmail.com
Website : https://jinnienichapa.github.io/website/index.html

Location : *Bangkok, Thailand*

Education
2016-2021 : Horwang School

2025 : Meiji University, Tokyo, Japan, Exchange Program (Year 4, Semester 1)

2022-2026 : INDA, the International Program in Design and Architecture at the Faculty of Architecture, Chulalongkorn University
Expected Graduation : 2026

Skills
Advanced
: Rhino, Adobe Illustrator, Adobe Photoshop

Intermediate
: Blender, Twinmotion, Grasshopper

Basic
: AutoCAD, Unreal Engine, After Effects, SketchUp, QGIS

Language: *Thai, English*

Experience
Landmee Pop-Up Exhibition
: 3D modeling and conceptual design for exhibition.
Leica Pop-Up Exhibition
: Supported spatial setup and exhibition installation.
Tutor — FAC ArtCentre Studio
: portfolio and design thinking class for design and architecture students.

Design Interests
Parametric design, spatial experience, conceptual design

table of contents



01 Village in a City : Residential Project



02 Living Heritage : Interior Project




03 Flow : Museum



04 Let it Float : Observation Tower



05 Invisible Boundaries : Extrastatecraft

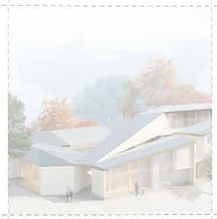


06 From Street to Neighbourhood : Mix-used building

01

Village in a City

Y3 S1
Brief: Urban Incubators
Program: AI, PS, Rhino

Village in a City is a Thai modern residential project located in the heart of Ploenchit, an area surrounded by high-rise and mixed-use buildings that blend work and living spaces seamlessly. The project aims to break the norms of the area by mentioning new activities, creating a space for relaxation and community gatherings, staying true to the original spirit of the neighborhood. The design emphasizes cultural exchange, reflecting the diverse population brought by the embassies in the vicinity. Sports and parks are utilized as connectors. The residences are designed to accommodate both locals and foreigners.

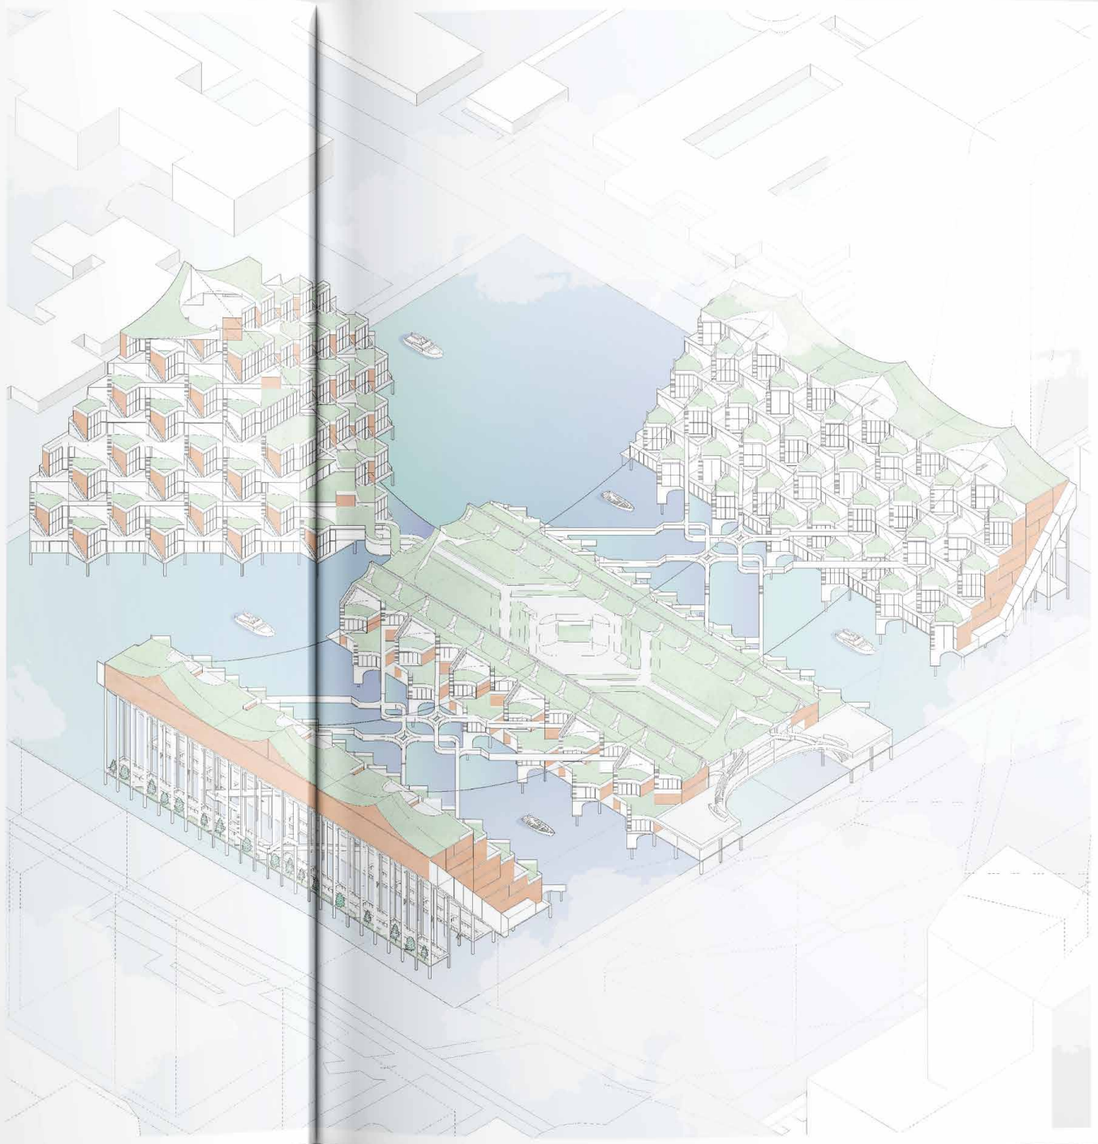

OLD BRITISH EMBASSY

PLOENCHIT, BANGKOK







FLOW

PARK AREA

SITE PLAN

scale 1 : 4000

0 62.5 125 250 500m

FIGURE GROUND MAP

scale 1 : 4000

0 62.5 125 250 500m

The figure ground map of the Ploenchit area highlights the distribution of shopping malls as dominant volumes, revealing how a few, development-ready sites structure the commercial core of the city. The dense cluster of malls, offices, and high-rise buildings reflects a mixed-income public and commercial activities and tourist destination.


BUILDING TYPES



office


residential

commercial

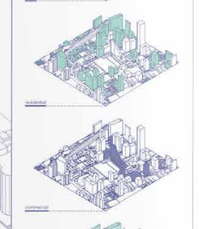


AXONOMETRIC


Around the Old British Embassy area in Phaya Thai, Ploenchit, Ratchadamri, and Sukhumvit, a clear hierarchy of different building types, ranging from mixed-use towers to low-rise residential blocks, can be observed. This axonometric view illustrates the spatial relationships between these typologies, highlighting their varying heights, densities, and functional distributions. The diagram reveals how commercial and residential buildings are interspersed, creating a dynamic urban fabric that reflects the area's role as a vibrant, multi-use district in the heart of Bangkok.

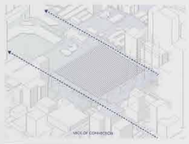


VAULT OF CONNECTIONS

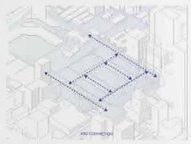


HEBO CONNECTIONS

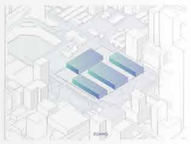


RAMPS

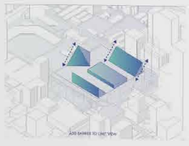


AXIS SHIFTED TO UNIT VIEW

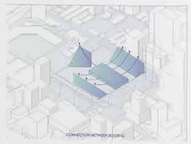



CONNECTION METHODS DIAGRAM

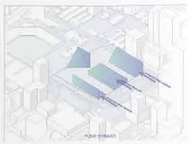



PUBLIC SYNAGOGUE

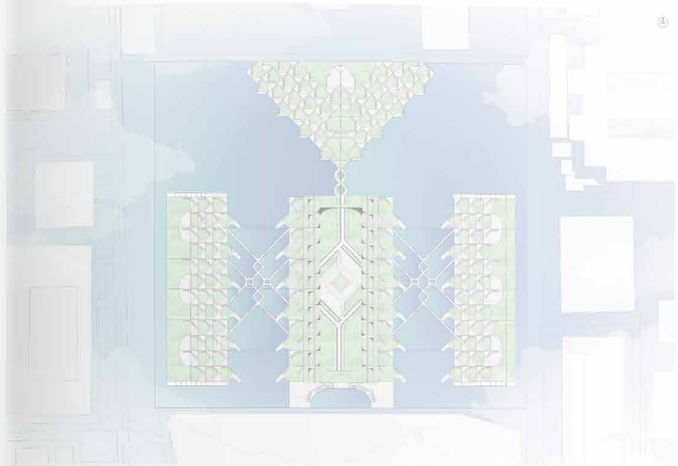

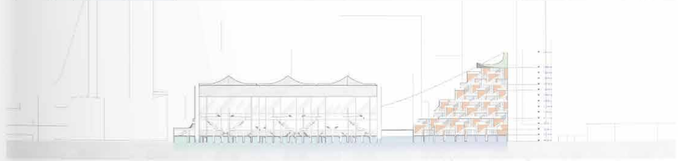


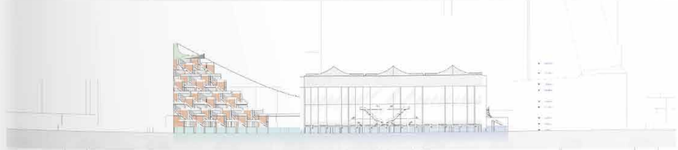

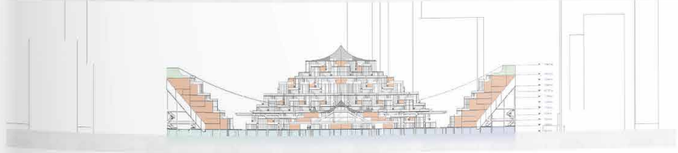

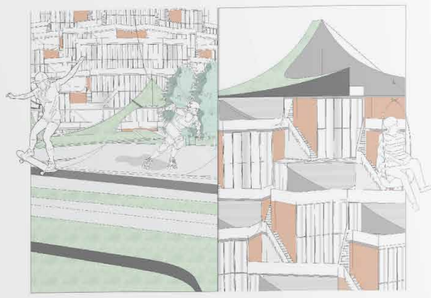





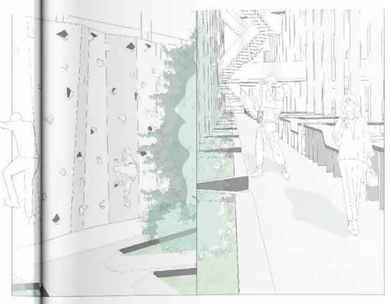

Due to its location surrounded by numerous embassies, the unit layouts are designed to cater to a variety of cultures. Each unit has been designed differently based on the needs of its residents, whether local or foreign, creating a diverse and inclusive residential community. The design thoughtfully incorporates elements that reflect the preferences and cultural influences of the occupants, ensuring a personalized and adaptable living experience. There are five types of units, with three main types located in the domestic area. At the top of this area is a communal park that can be used by both residents and the public. The private and public spaces are separated by distinct levels to maintain privacy while encouraging interaction. To support the concept of using parks as areas for cultural exchange, each unit is also designed with its own green roof, providing additional greenery and promoting sustainability.



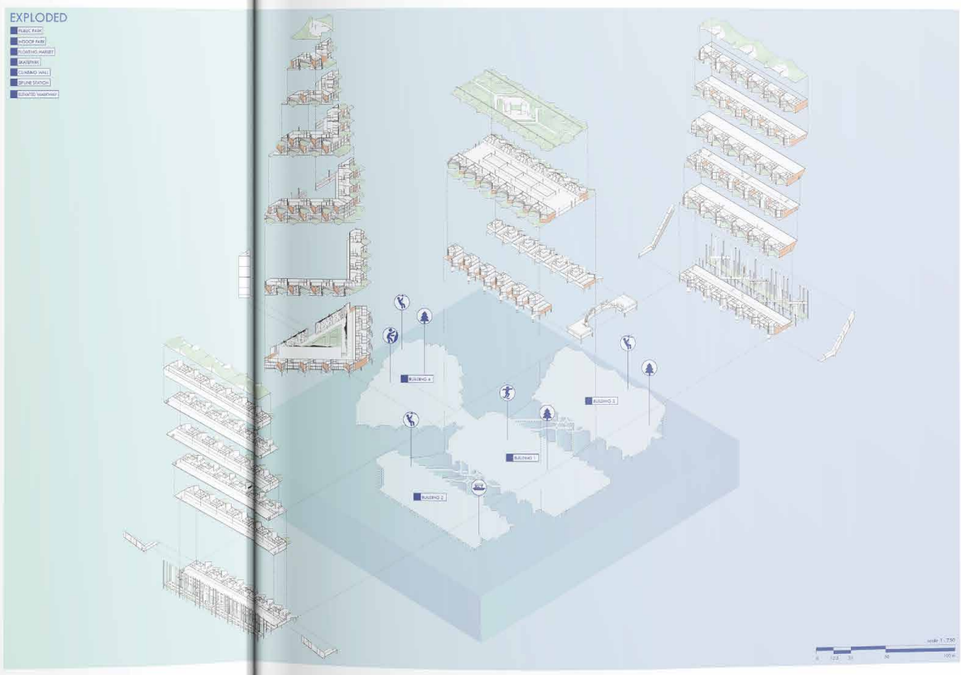

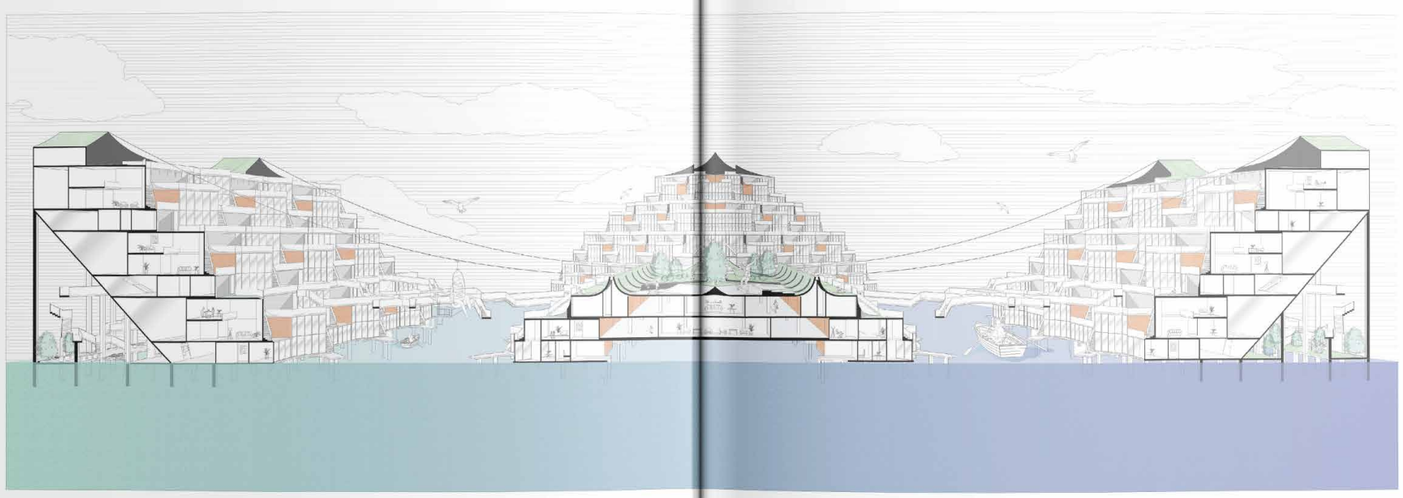

02

Living Heritage

a culinary sanctuary in Kudi Chin

Y4 S2
Brief: Retro-Pedagogies
Program: AI, PS, Rhino, Blender, Autocad, Sketchup


Living Heritage, a culinary sanctuary in Kudichin. Located in Kudi Chin, a neighborhood defined by the coexistence of diverse cultures and religions, this project investigates how architecture can facilitate pedagogical exchange through culinary practices. The proposal positions the house as a platform for both experiential and participatory learning, where locals engage with foreigners and Thai adults through shared cooking activities.The architecture creates an environment where knowledge is not only taught, but lived, practiced, and shared enabling exchange beyond the boundaries of language and belief.








Located within Windsor House, this project explores how architecture can shape learning behavior through a pedagogical approach centered on culinary practices. The proposal introduces a culinary school where local residents share knowledge with foreigners and Thai adults through cooking as a common language. The architecture reinterprets Thai-Portuguese identity through the use of timber, tiles, fabrics, and weaving patterns. Furniture design follows Thai traditional floor-based living, promoting eye-level equality.

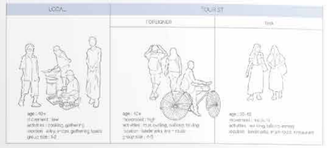










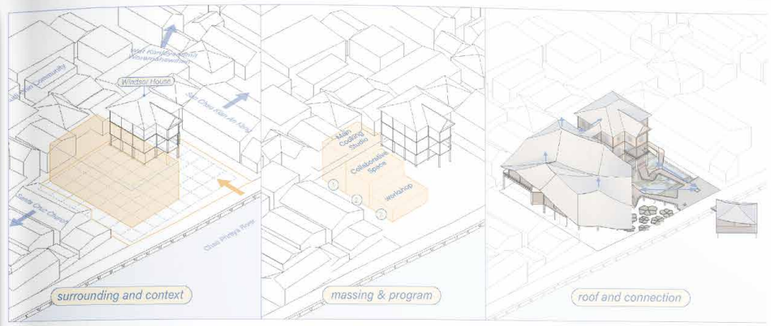

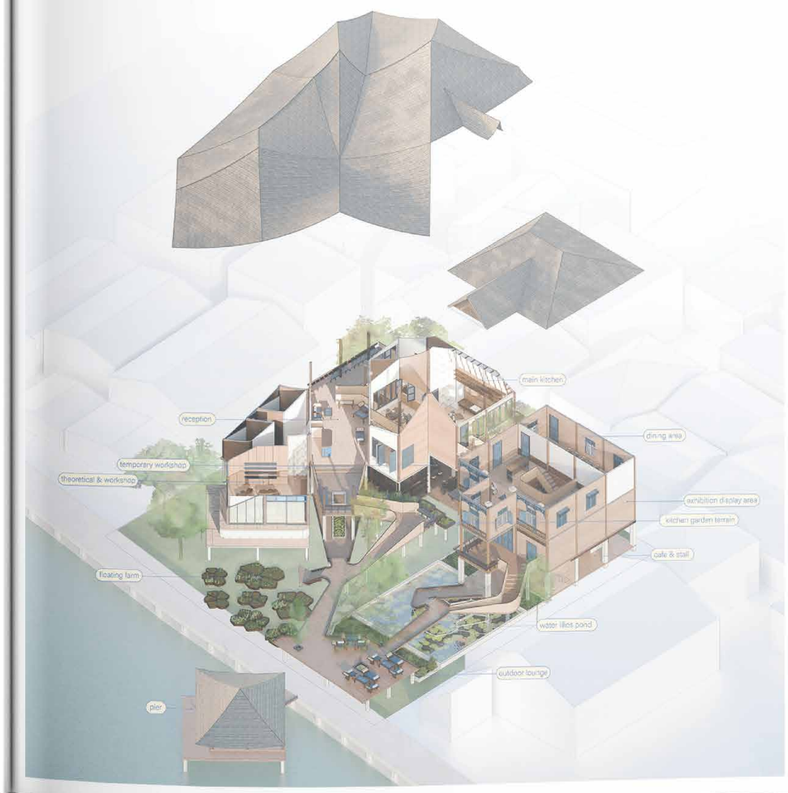

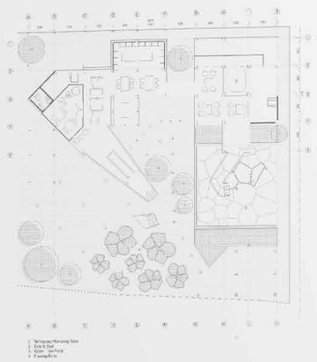

ground floor

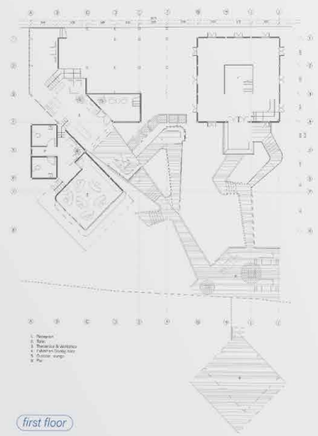

first floor




second floor






The project is divided into two systems: a new extension for program-based learning, including workshops and a main kitchen studio, and the preserved house for experience-based learning through dining, observation, and cultural interaction. Together, these spaces create an environment where knowledge is not only taught, but lived, practiced, and shared beyond language and belief. Cooking becomes a pedagogical tool—knowledge is transmitted through hands-on practice, storytelling, and repetition. The kitchen is not enclosed; it is visually open, allowing learners to observe techniques before participating.


03
Flow

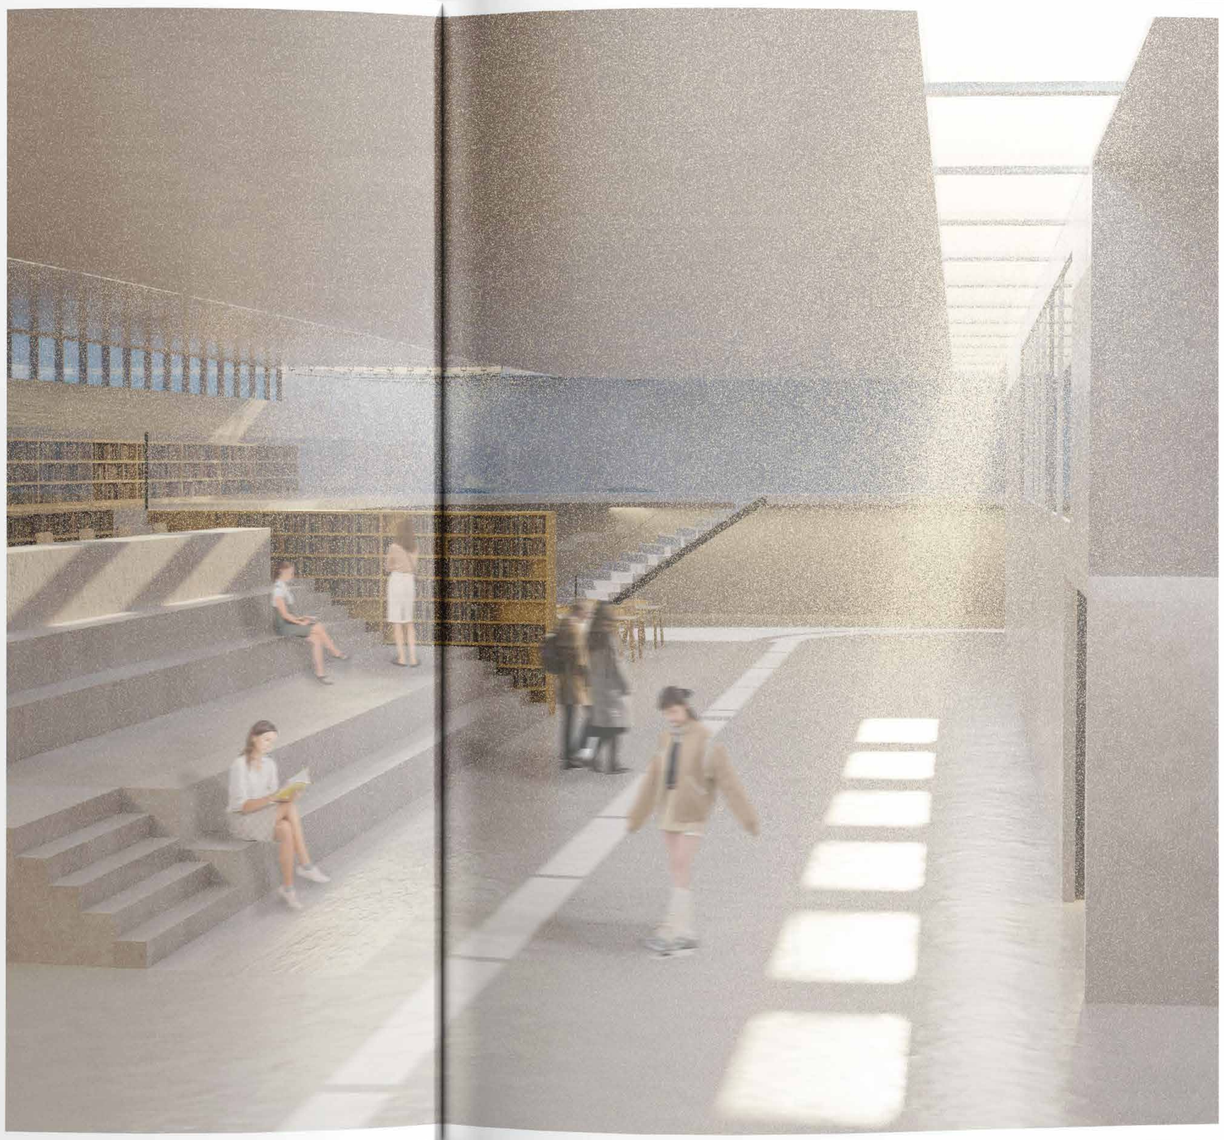



Y2 S2
Brief: Aquatecture
Program: Rhino, Blender, Ai, Ps

Flow is an underground living museum that highlights the importance of land use through many eras related to the waterway. The museum is placed in the underground level as an extension of Phayathai palace. It's different from the current museum in that it's a living museum people can experience through activities. The key concept is using the ground level to separate the timeline. In this area, water is the main factor that evokes the Ratchathewi area, but these days the importance of the waterway is lost. Flow is also created to bring back attention to the waterway.

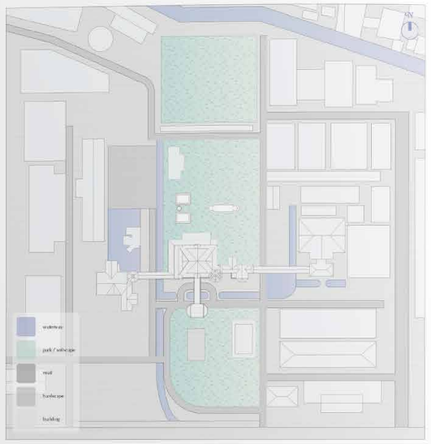

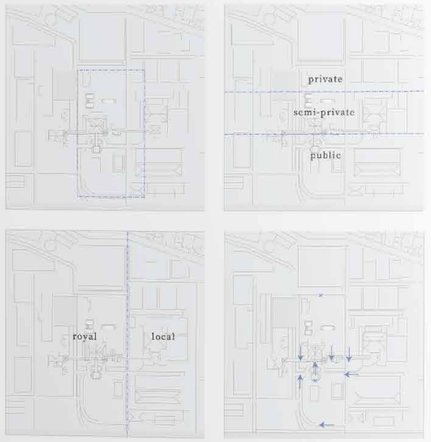

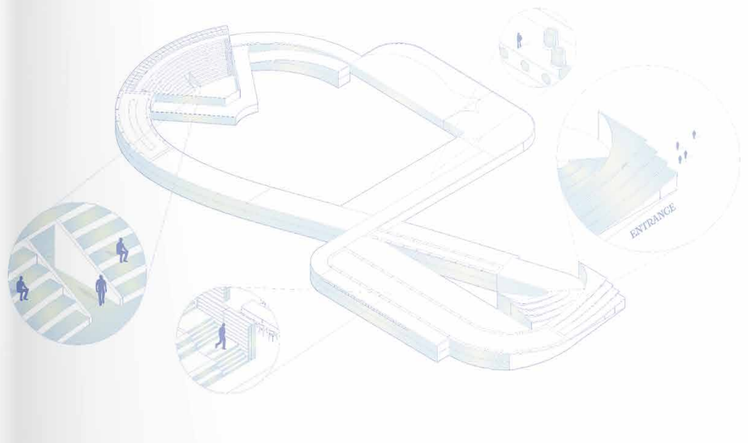

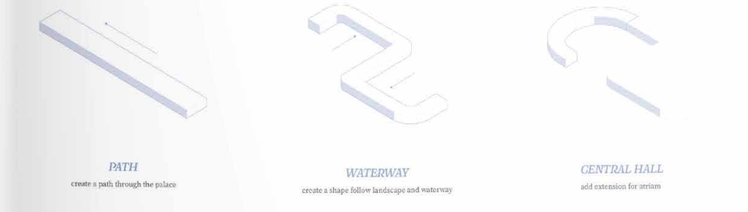

PATH
create a path through the palace

WATERWAY
create a shape follow landscape and waterway


CENTRAL HALL
add extension for atrium





GREATE A LOOP
connext both side to create a loop

DEFINE
define level for normal ground and underground

EXTENSION
extension on both width and floor level due to the use

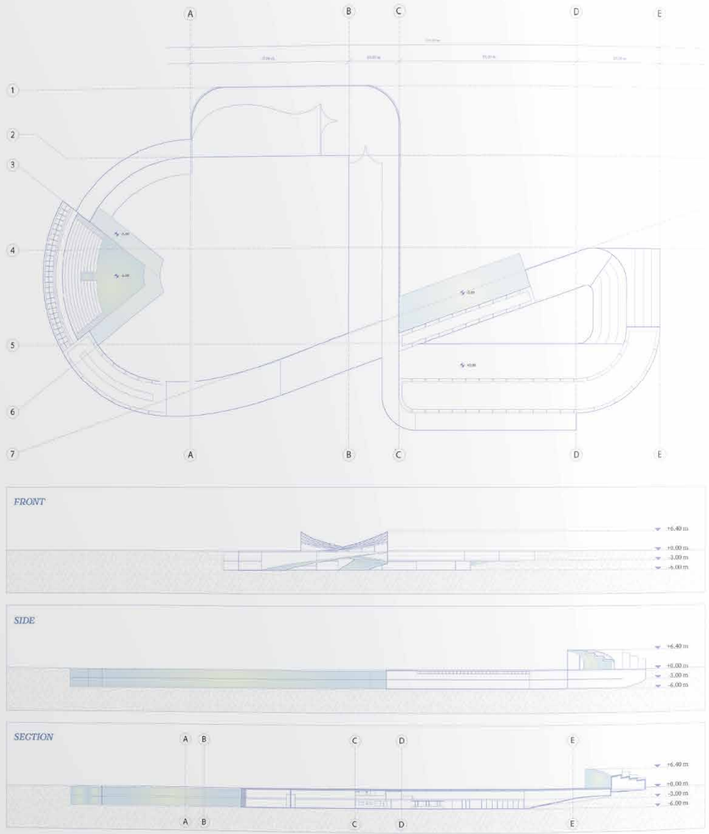
A
B
C
D
E
1
2
3
4
5
6
7
FRONT
+6,40 m
+0,00 m
-3,00 m
-6,00 m
SIDE
+6,40 m
+0,00 m
-3,00 m
-6,00 m
SECTION
+6,40 m
+0,00 m
-3,00 m
-6,00 m

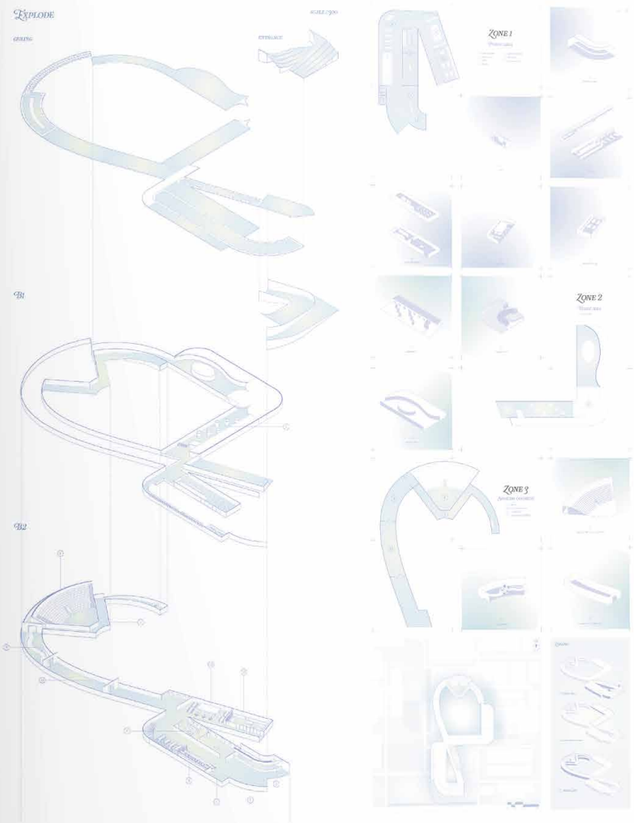
EXPLODE
ZONE 1
ZONE 2
ZONE 3

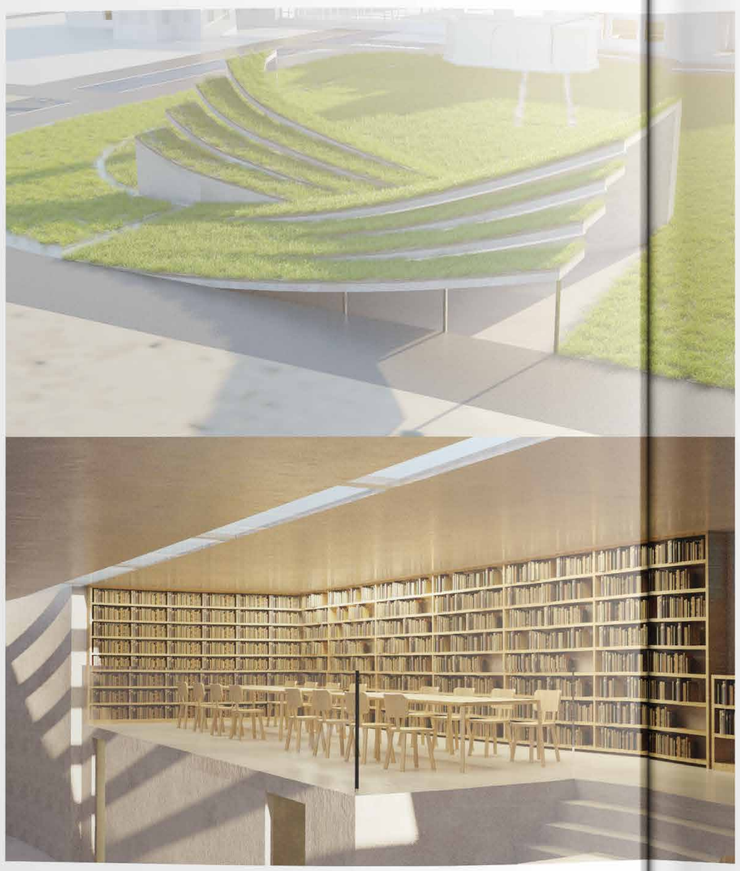









04
Let it Float

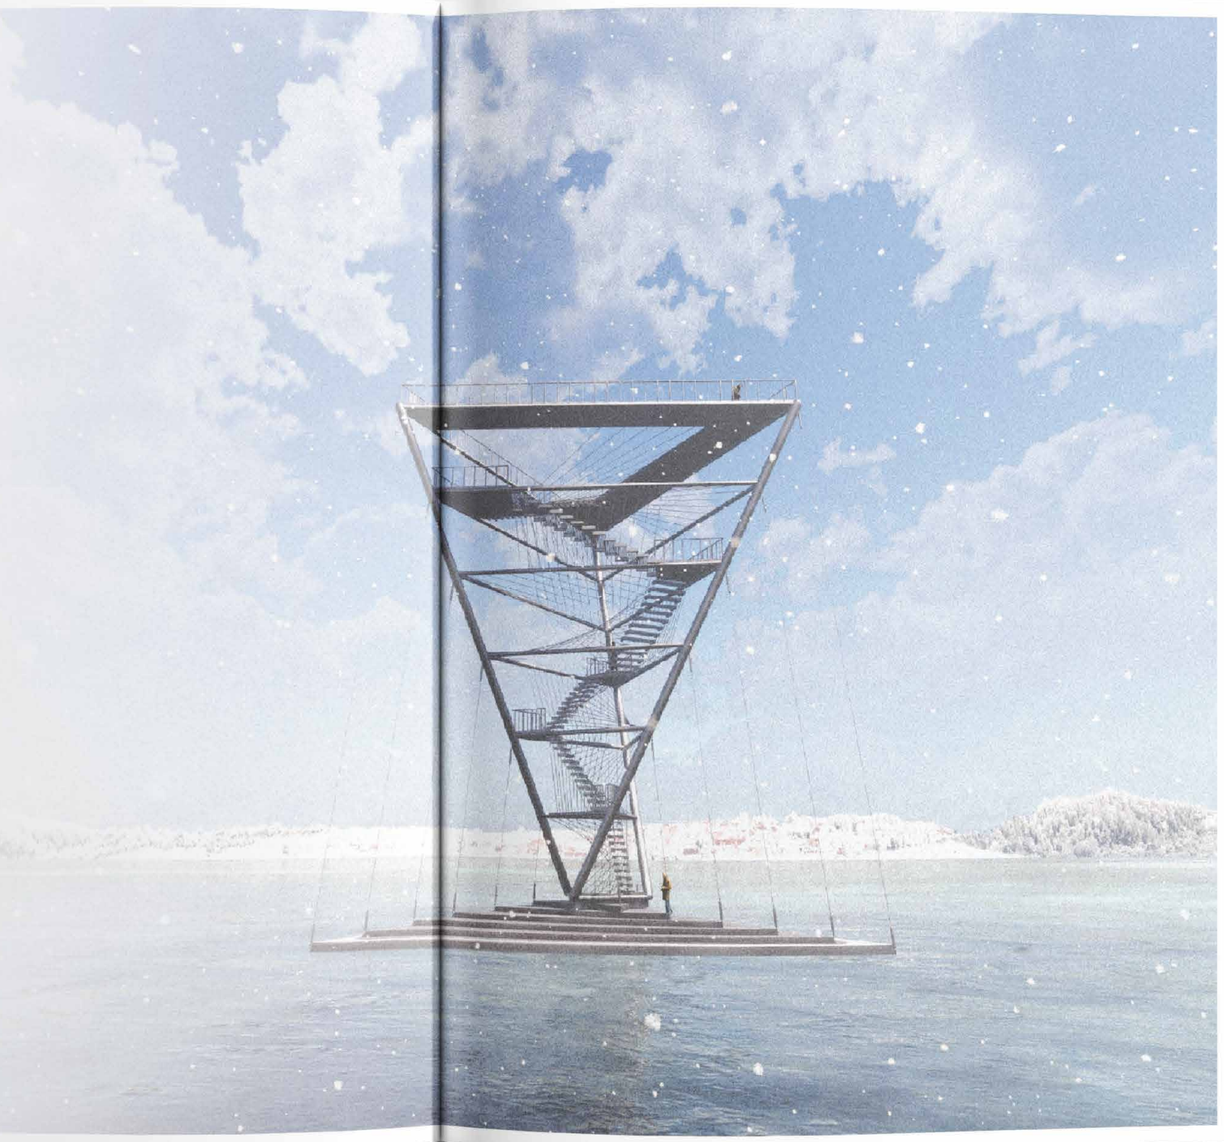

Y2 S1
Brief: Towards an Ecosystemic Revolution
Program: Rhino, Blender, Grasshopper, Ai, Ps, Ae, Twinmotion

"Let It Float" is a project that aims to create a waterfowl observation tower based on the concept of the differences in waterfowl activities related to height. The tower also highlights the culture of this area, which includes observing ducks migrating and the importance of the wetlands area in De Smet. The building has two main functions: "twist" and "float." These two functions are connected and work by using the water flow of the lake to make a change to the tower. The tower was twisted to follow the migration route.

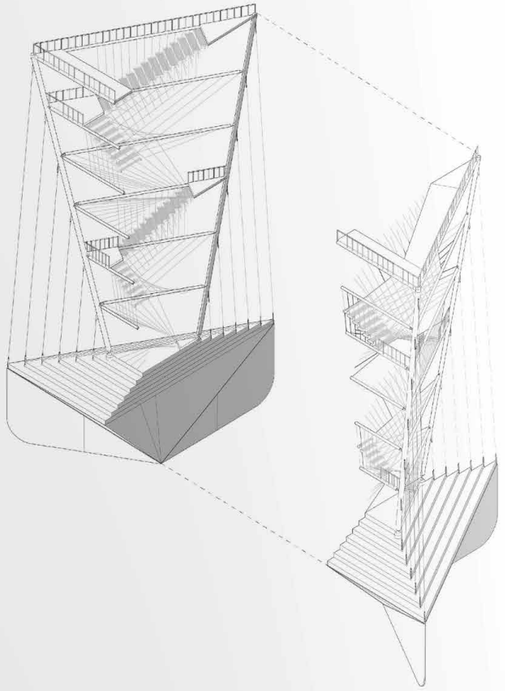


+ tension wire rope





+ hinge and pin connections
+ welding technique

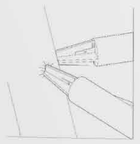



+ ball joint








+ hanging stair

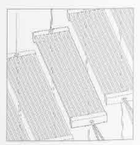

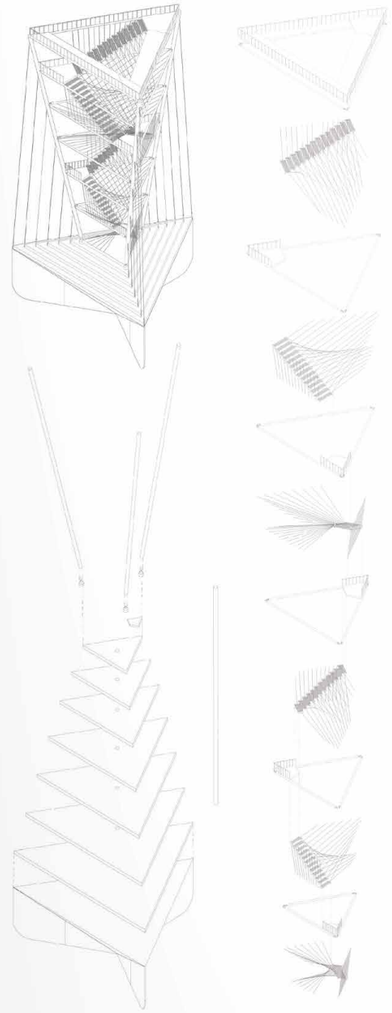

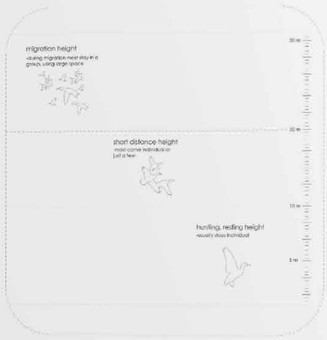

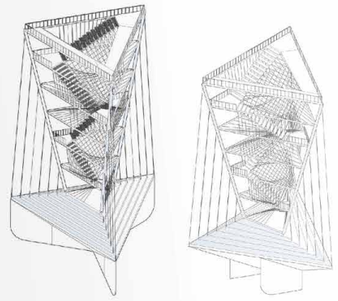

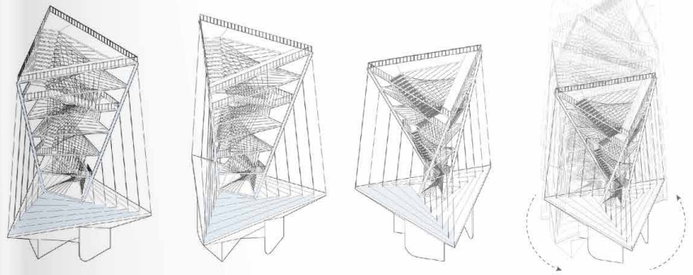

Building form follows waterfowl activities height. The building has a height of 30 m which is the lowest height for ducks migration, and around 10-20m is a height that duck flys in short distance. Last one is 5 m, it's a resting and hunting height .

The main design of the tower is the twist function, which works on the whole building with the control of the main pipe. First, it twists to a framed view following the migration route. Second, there are differences in duck activities during the summer and winter. In summer, ducks usually migrate, so tall buildings would be suitable for them, while in the winter they usually take a break and stay on the land. Lastly, to create a variety of views for the visitor and enjoy observing duck activities from different heights. The tower start to twists between gap of summer to winter. Tower twisted up to 120 degree . And when the tower twist the height also decrease. From the calculation the height change 1 meter effect to 17.2 degree.

05


Invisible Boundaries

Rewilding Urban Zones in the Post-Anthropocene




Y3 S2
Brief: Extrastetecraft
Program: Unreal Engine, Rhino, Grasshopper, Blender, Qgis, Ai, Ps, Ae

Invisible Boundaries act as an infrastructure that invites wildlife back to the city area, using it as an asset to bring nature into urban life. The project focuses on rewilding spaces and redefining the relationship between cities and nature. Instead of decoration, nature becomes part of daily life, creating shared spaces for humans and wildlife through four key invisible boundary methods:

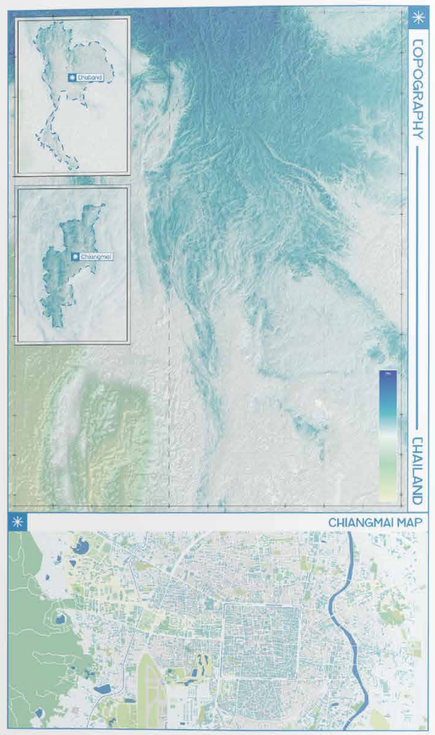

The project questions how we can introduce wildlife into spaces where most of the city is owned by humans. If we want to create a shared space, then how would we share a space. This leads to the idea of creating a new infrastructure as a terrain itself, using invisible boundaries both human-made and natural as connections that blend seamlessly. Ruins are introduced as key assets, following the Barry Walk concept of integrating nature into hybrid urban design. In the city, ruins make the most sense as they naturally invite plant growth, with grass and vegetation reclaiming these structures over time.

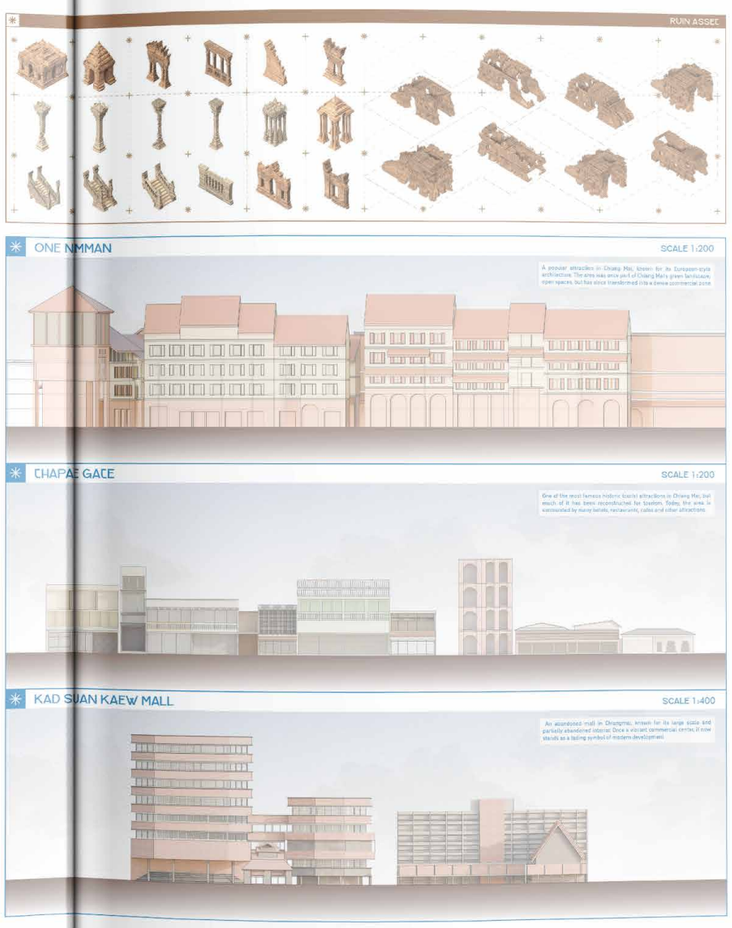


ONE NIMMAN

PLAN



SIDE

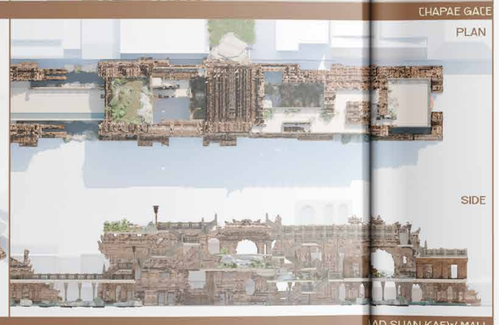


AXONOMETRIC



CHAPAE GATE

PLAN

SIDE

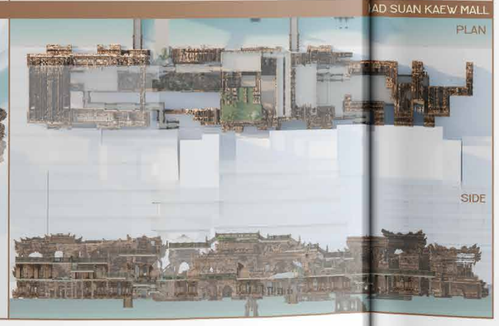

AXONOMETRIC



AD SUAN KAEW MALL

PLAN


SIDE






KAD SUAN KAEW MALL
Elevation Boundaries
Fluid Boundaries


CHAPAE GATE
Elevation Boundaries
Vegetation Boundaries

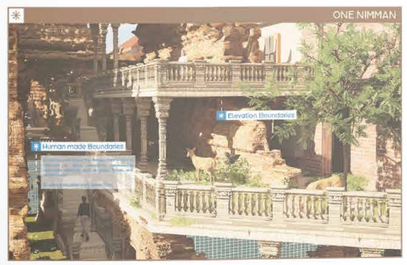
ONE NIMMAN
Elevation Boundaries
Human made Boundaries

06

From Street to Neighbourhood

Y4 S1
Brief: Pattern Language
Program: Rhino, Blender, Qgis, Ai, Ps,


From Street to Neighbourhood: A Field of Fragments is a mixed-use project in the Harajuku–Omotesando area that activates the plot by reassembling fragments from the existing urban context. The project creates a smooth transition between commercial and residential areas while maintaining clear boundaries between the two.



Pattern Language


brings the existing element that found in the site to create a strategies to apply for the new build

Urban Skin and Core

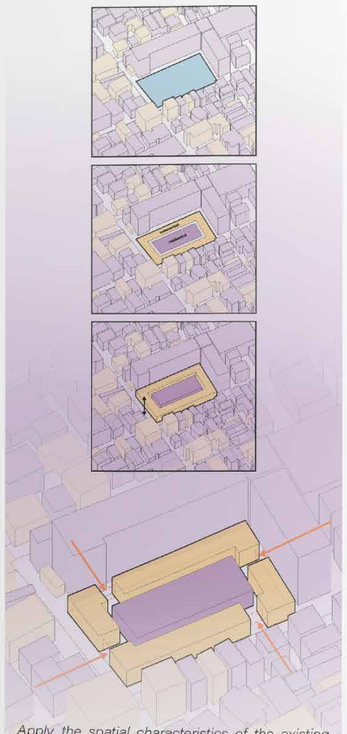


Apply the spatial characteristics of the existing building plots from the more active route to the site and its surrounding areas. By adapting the successful mix of commercial "skin" and residential "core," the design aims to activate the less frequented route and enhance pedestrian flow through the site.

Field of Fragments

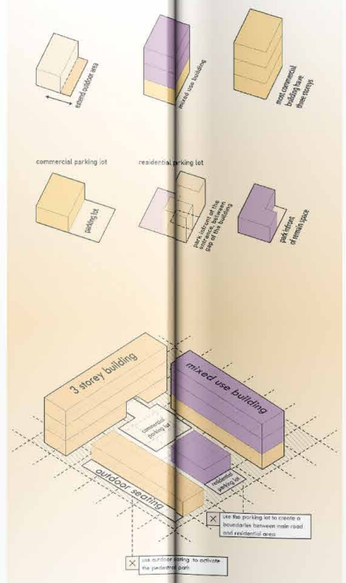



This strategy activates the block by reorganizing the plot layout using existing efficient elements observed from the site. Yet, these could be rearranged following the position of each block. Through this configuration, fragmented plots are transformed into a more active urban block.

Topographic Mass Adaptation

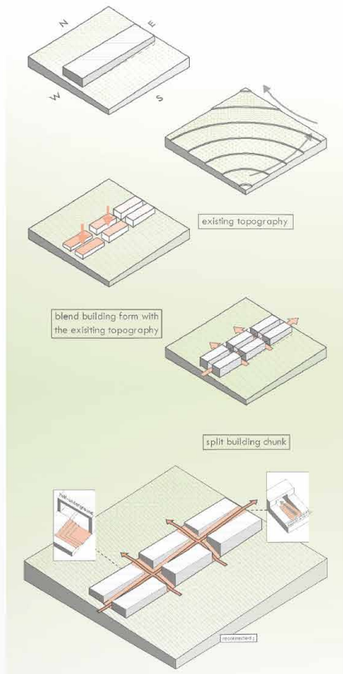

Reconfigure large building masses by splitting them to create new pedestrian paths that link the main road to interior alleys. The architecture itself becomes a transitional device, adapting itself to the existing topography.

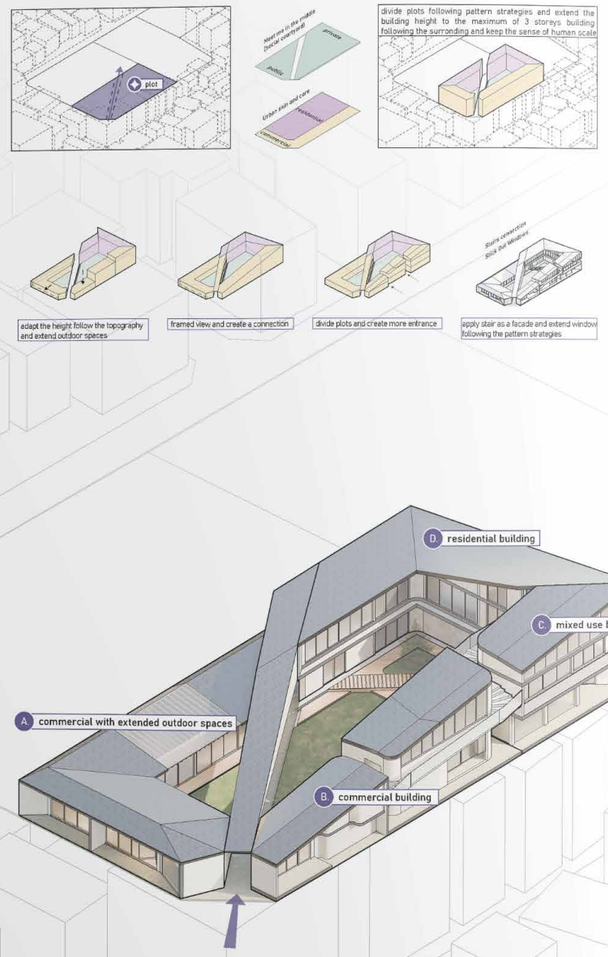
plot
Heart of the village
Urban main and core
private
public
residential
commercial
divide plots following pattern strategies and extend the building height to the maximum of 3 storeys building following the surronding and keep the sense of human scale
adapt the height follow the topography and extend outdoor spaces
framed view and create a connection
divide plots and create more entrance
Stairs connection
Stick for Mediation
apply stair as a facade and extend window following the pattern strategies
D residential building
C mixed use building
A commercial with extended outdoor spaces
B commercial building

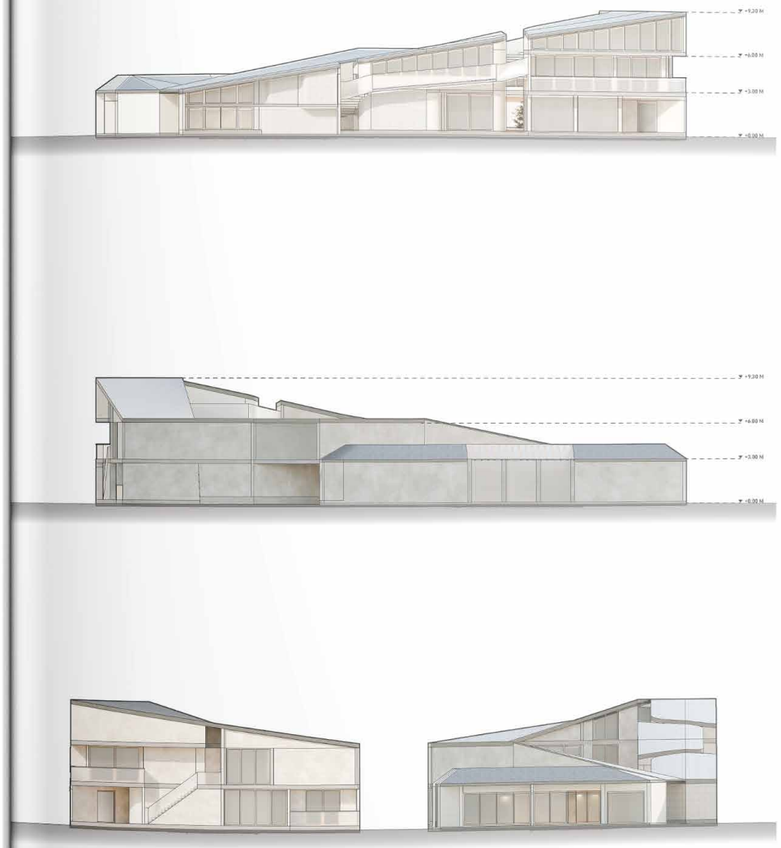

+9.20 M
+6.00 M
+3.00 M
±0.00 M


ONLY HUMAN STUDIO


Architectural Intern · Bangkok · 2026

A design studio working across architecture, interior, furniture, and structural design. The internship involved contributing to different stages of projects across a range of building types, including residential, parking garages, clinics, and cafés. Tasks included interior layouts, furniture design, lighting and material selection, structural modelling, technical drawings, diagrams, rendering, model making, and site visits.

The experience focused on human-centered design and attention to detail, exploring how proportions can be adapted to actual use and how materials, structure, and construction details shape the quality of a space.

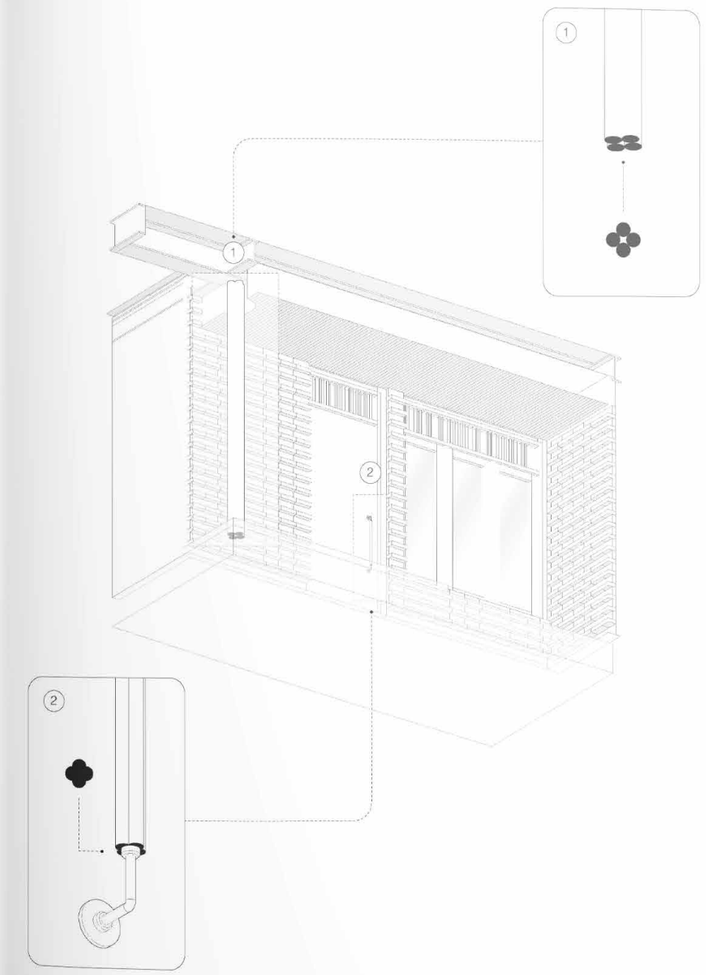

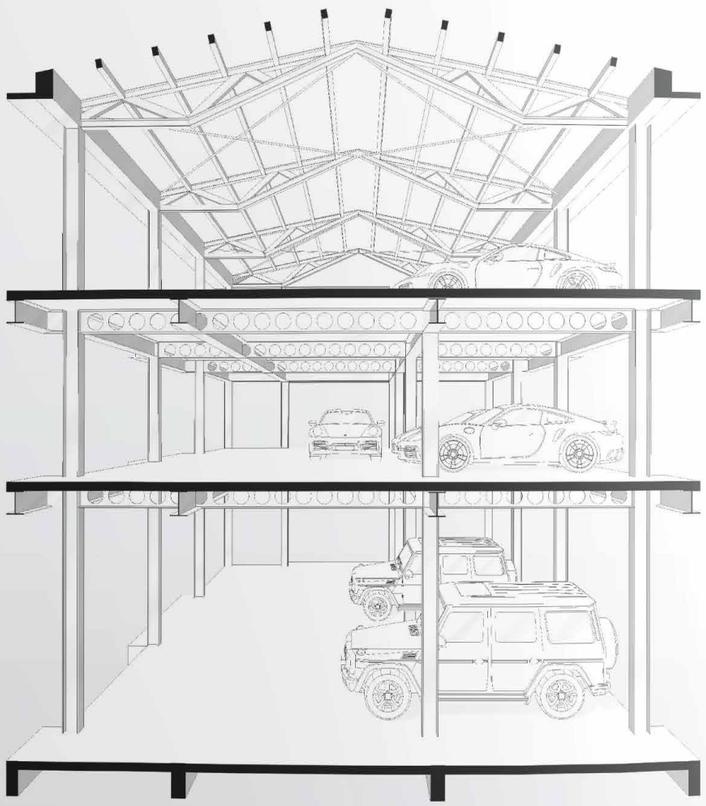

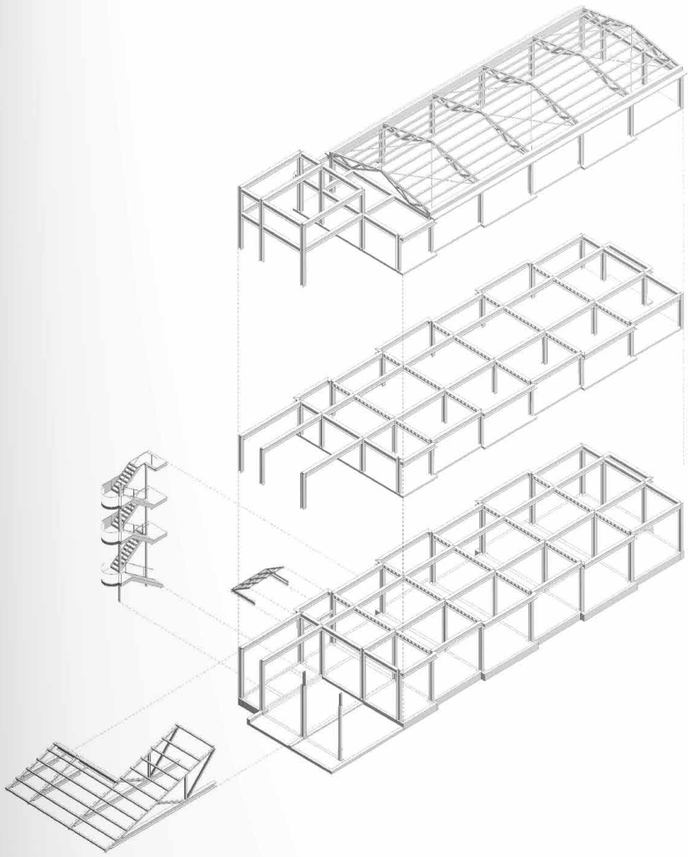

25G GARAGE — STRUCTURAL MODELLING & DIAGRAMS

Developed a 3D structural model from engineering drawings, studying the building's structural system, connections, and assembly from ground to roof. Translated the model into diagrams to communicate the structure and improve understanding of how individual components come together.

The garage uses a steel structure with cellular beams, where the shifted form creates slitted voids that allow indirect natural light into the space. In contrast, the office and residential buildings adopt a simple reinforced concrete grid, with structural elements left exposed to express their material character.



NNW CLOTHING STORE — INTERIOR DESIGN
Contributed to interior and furniture design, spatial layout, lighting, 3D modelling, and render visualization, with a focus on minimalist industrial elements and the balance between simplicity, materiality, and detail.




NNW CAFE&RESRAURANT — FURNITURE DESIGN
Contributed to the design of furniture pieces, including chairs, tables, and counters, with a focus on material selection, simplicity, and attention to detail. Explored proportions and dimensions in relation to human use, as well as the restuarant layout.

03 Diagrams & Visual Communication

HOUSE P

Produced diagrams illustrating the renovation, highlighting changes to the building structure, layout, and interior design.

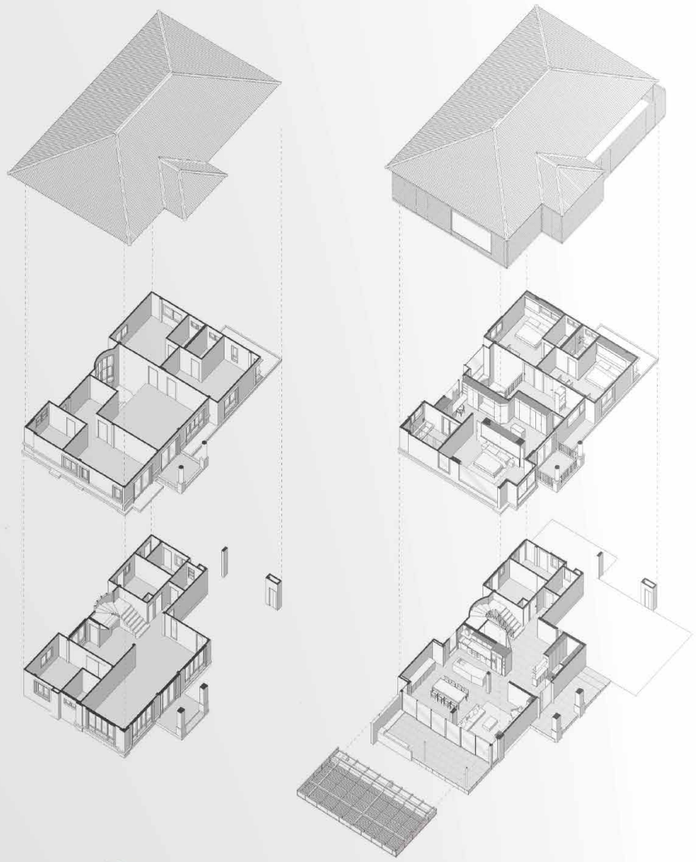

before

after

DWCR APARTMENT

Produced diagrams illustrating interior and furniture design, highlighting material selections, textures, and spatial details.



ASACHA MATCHA BAR

Illustrated furniture designs, material selections, and the overall interior design

